


PROPOSED RESIDENTIAL DEVELOPMENT
FIVE BEDROOM DUPLEX
AT
BAUCHI, STATE



MARCH, 2023

SITE PLAN

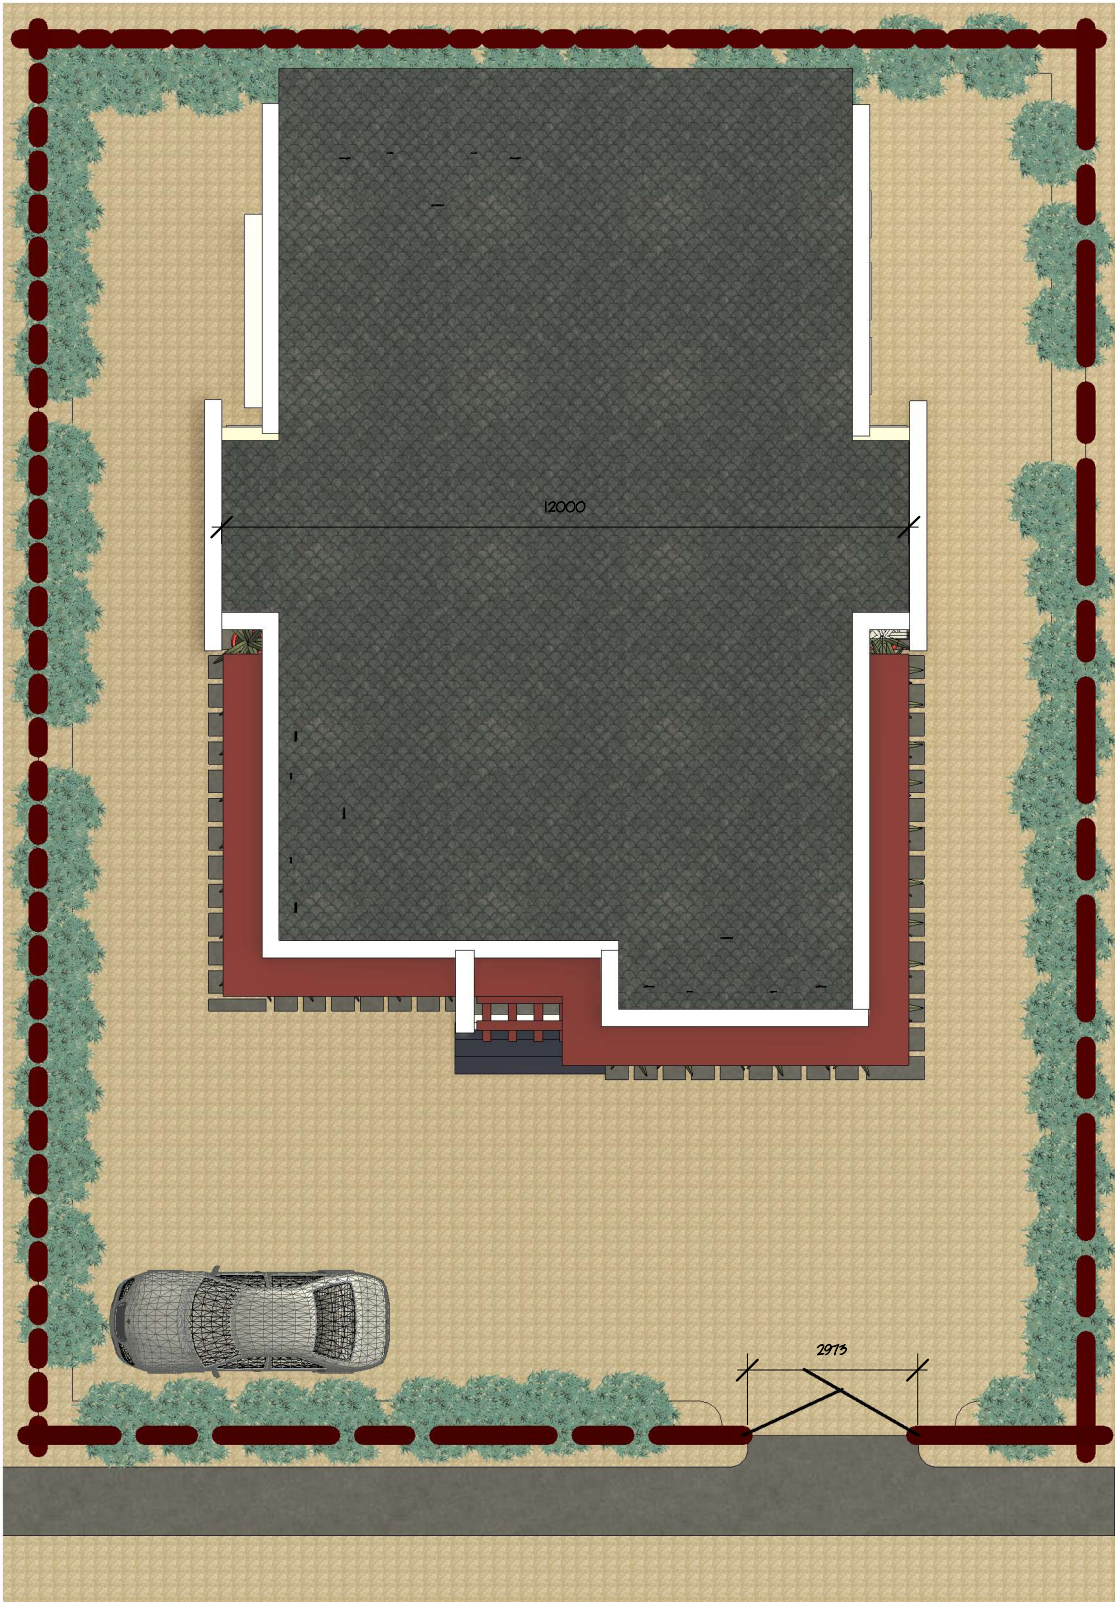

Notes:

Rev No.	Date	Description
---------	------	-------------

Revision No.

AFR/1175
RC:619405

SCYNA MATRIX LTD

ARCHITECTURE ENGINEERING CONSTRUCTION

8004, KADO MALL, AHMADU BELLO WAY, ABUJA, FCT

E-mail: scynamatrixltd@gmail.com

Tel: 08035951088, 09056554220

Project:

Project Name

Client:

Owner

Design by:

Designer

Drg. Title


SITE PLAN

Date	03/31/23
------	----------


Scale	1 : 120
-------	---------

Drg. No.

A100

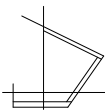

GROUND FLOOR

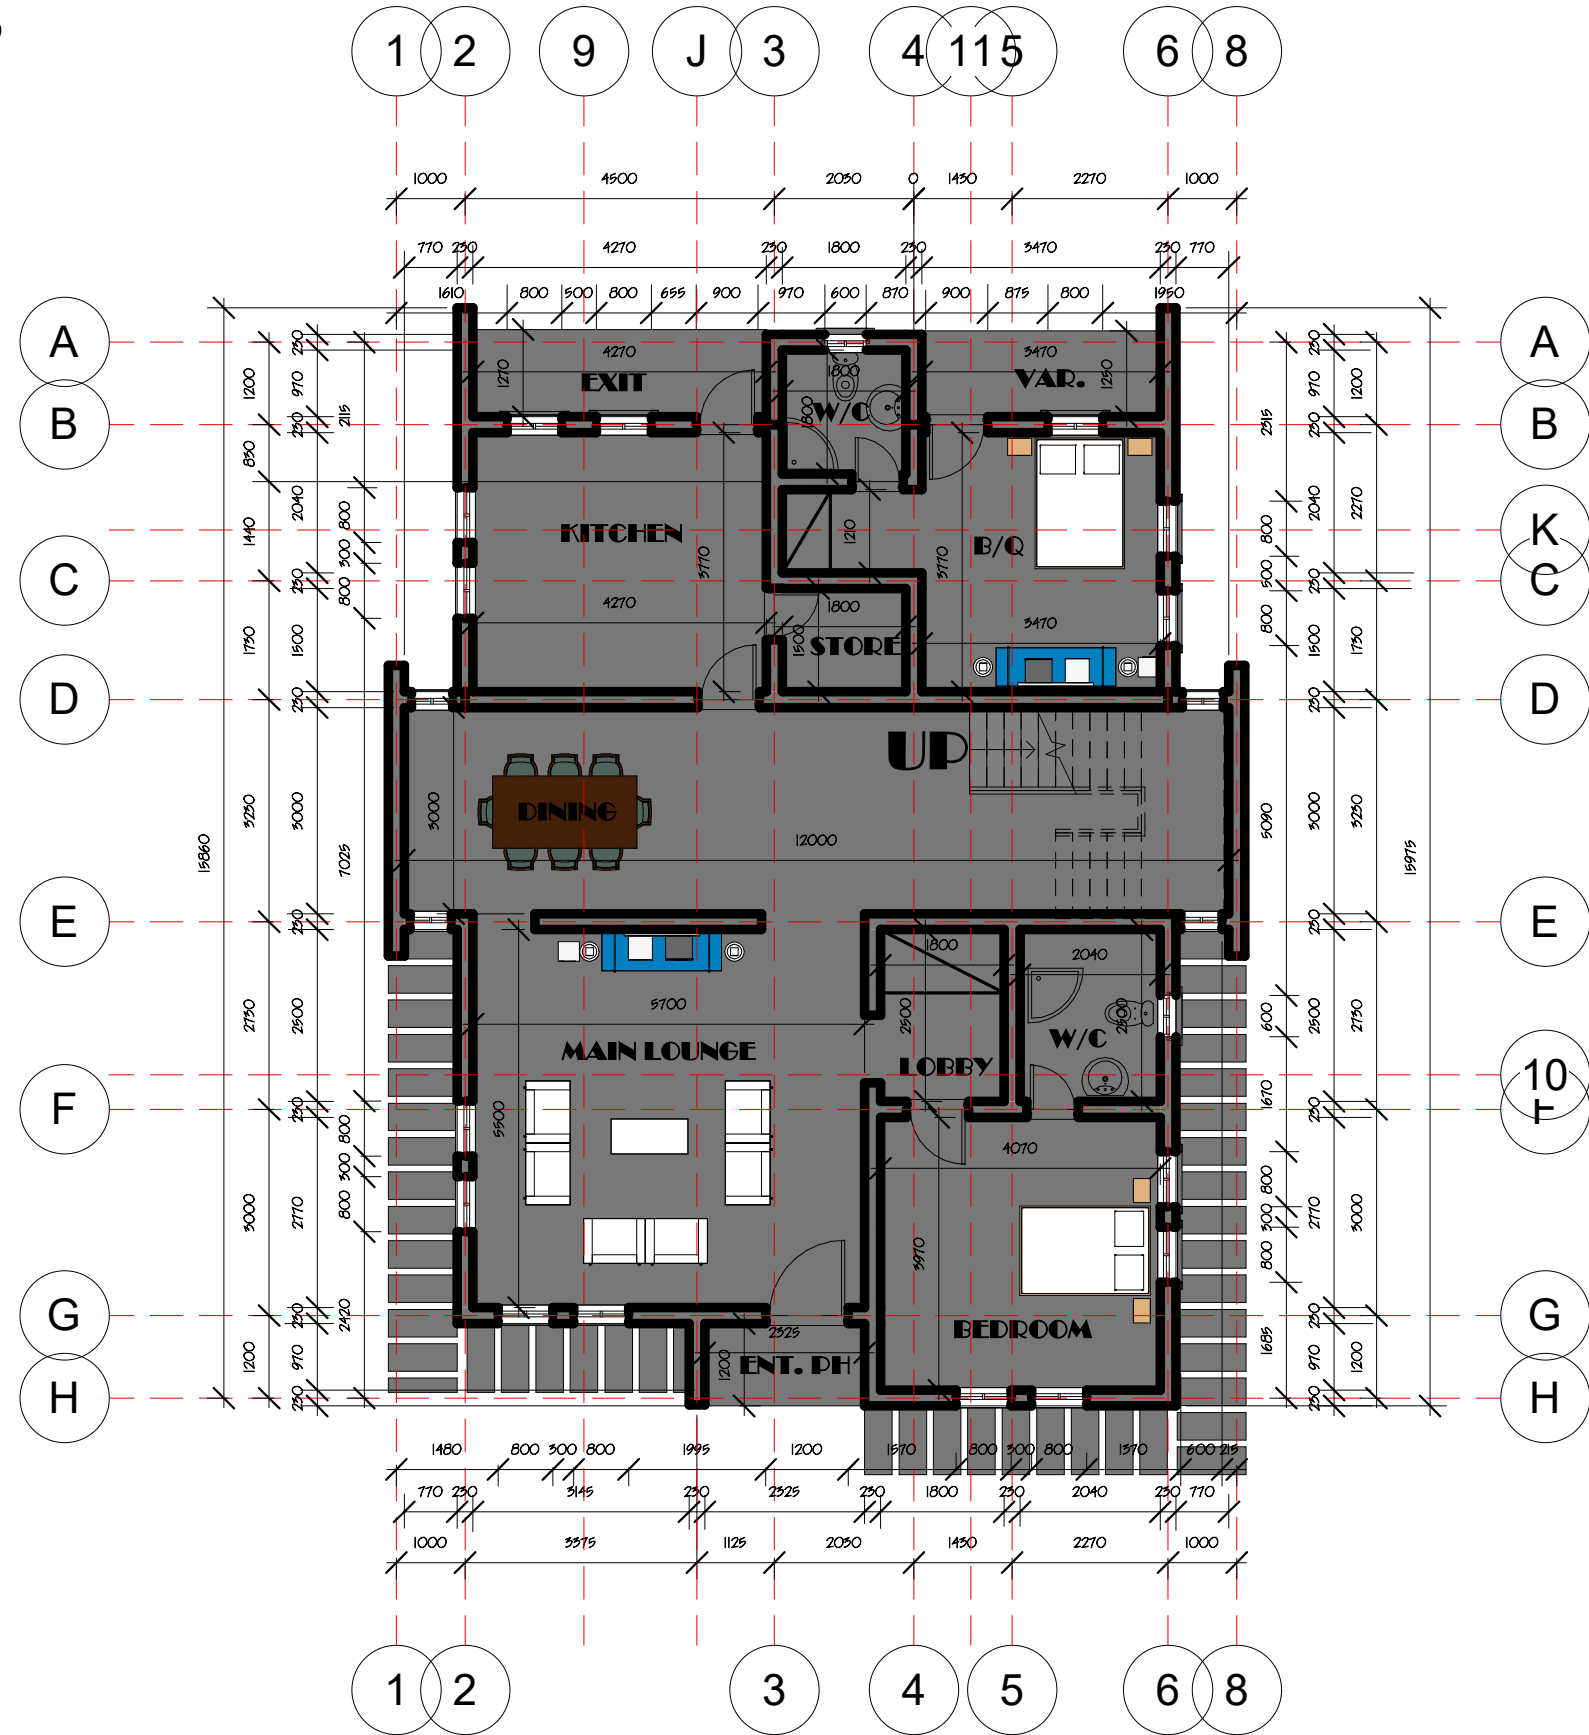

Notes:

Rev No.	Date	Description

Revision No.

AFR/1175
RC:619405

SCYNA MATRIX LTD
ARCHITECTURE ENGINEERING CONSTRUCTION
B004, KADO MALL, AHMADU BELLO WAY, ABUJA, FCT
E-mail: scynamatrixltd@gmail.com
Tel: 08035951088, 09056554220

Project:
Project Name

Client:
Owner

Design by:
Designer


Drg. Title
GROUND FLOOR

Date
07/29/22

Scale
1 : 100

Drg. No.
A101

FIRST FLOOR

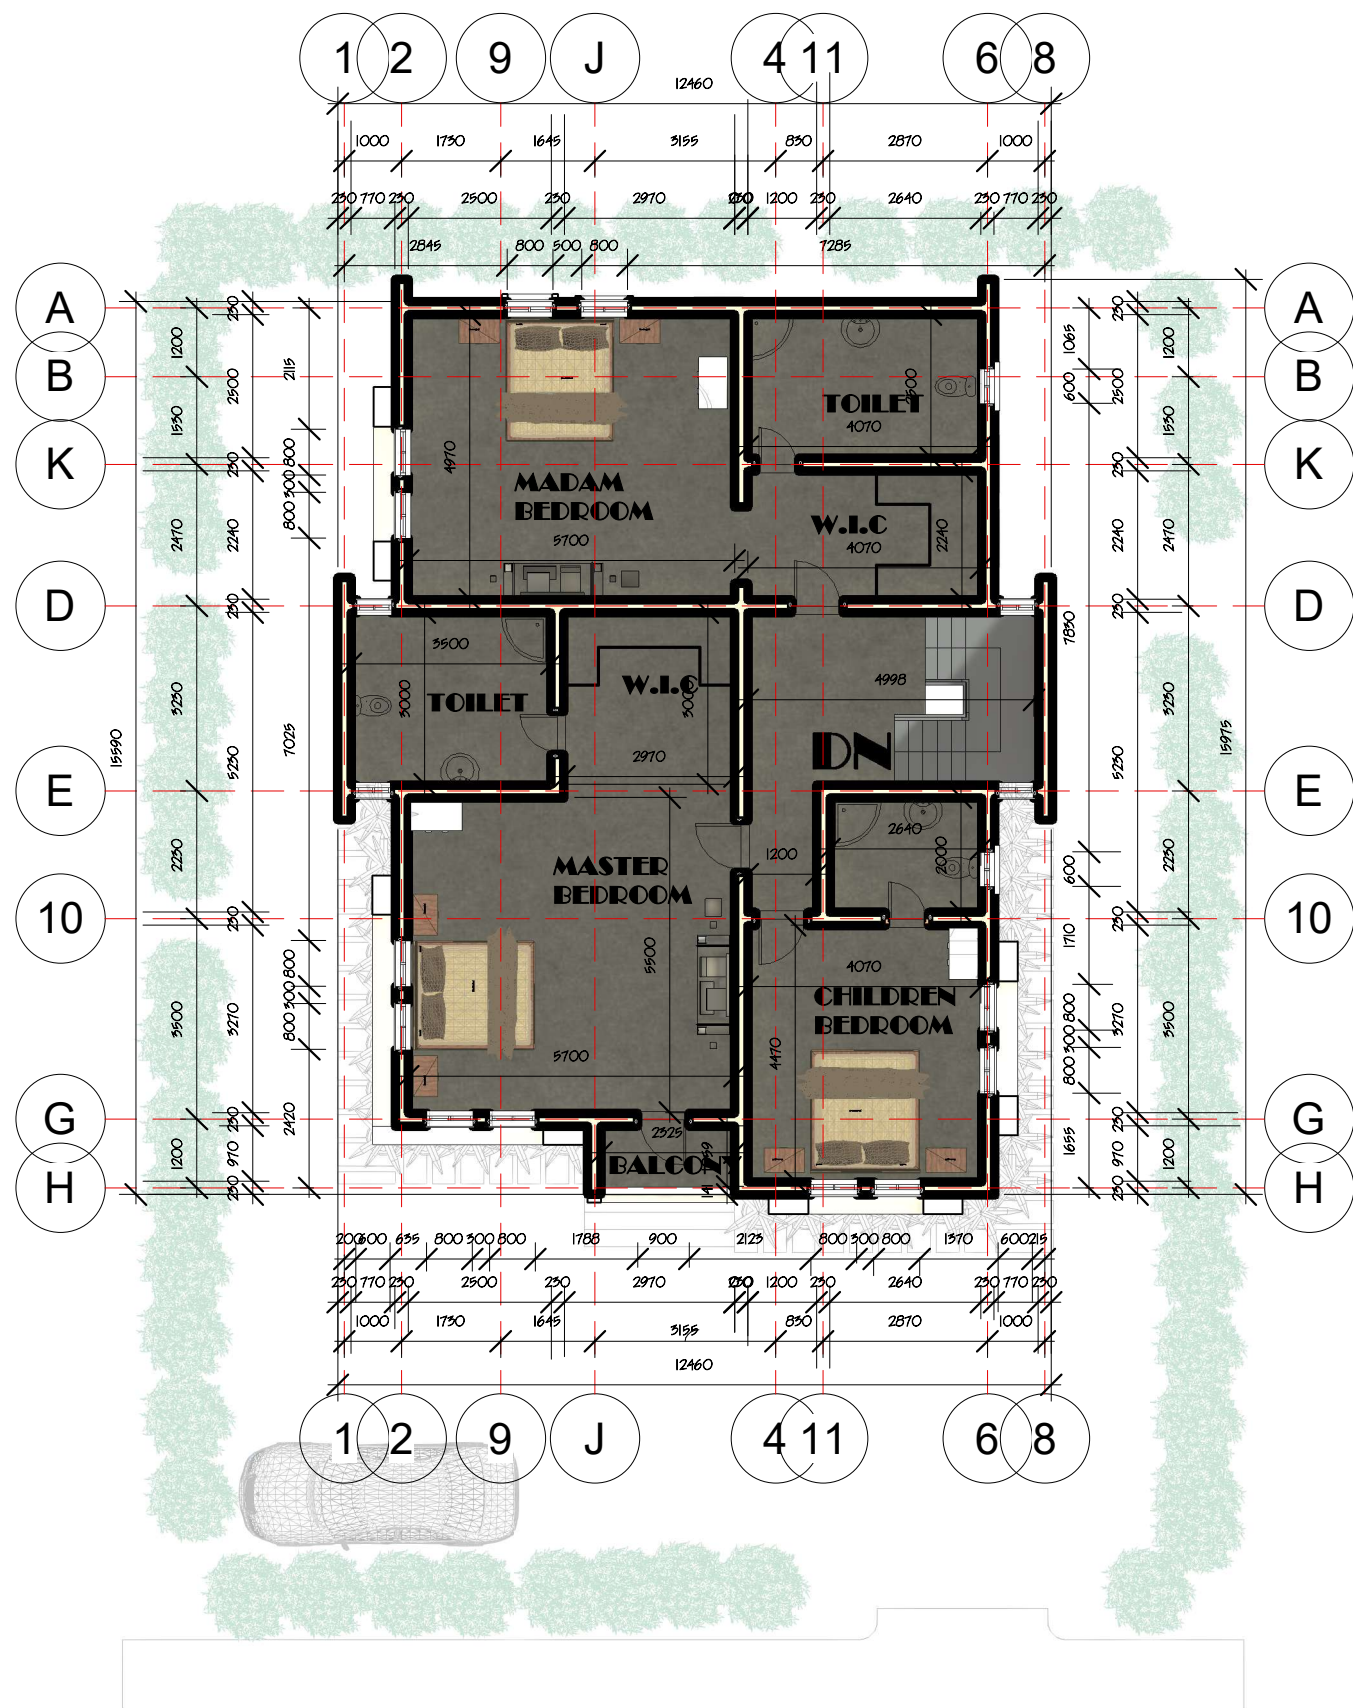

Notes:

Rev No.	Date	Description

Revision No.

AFR/1175
RC:619405

SCYNA MATRIX LTD
ARCHITECTURE ENGINEERING CONSTRUCTION
8004, KADO MALL, AHMADU BELLO WAY, ABUJA, FCT
E-mail: scynamatrixltd@gmail.com
Tel: 08035951088, 09056554220

Project:
Project Name

Client:
Owner

Design by:
Designer


Drg. Title
FIRST FLOOR

Date
07/29/22

Scale
1 : 120

Drg. No.
A102

ROOF PLAN

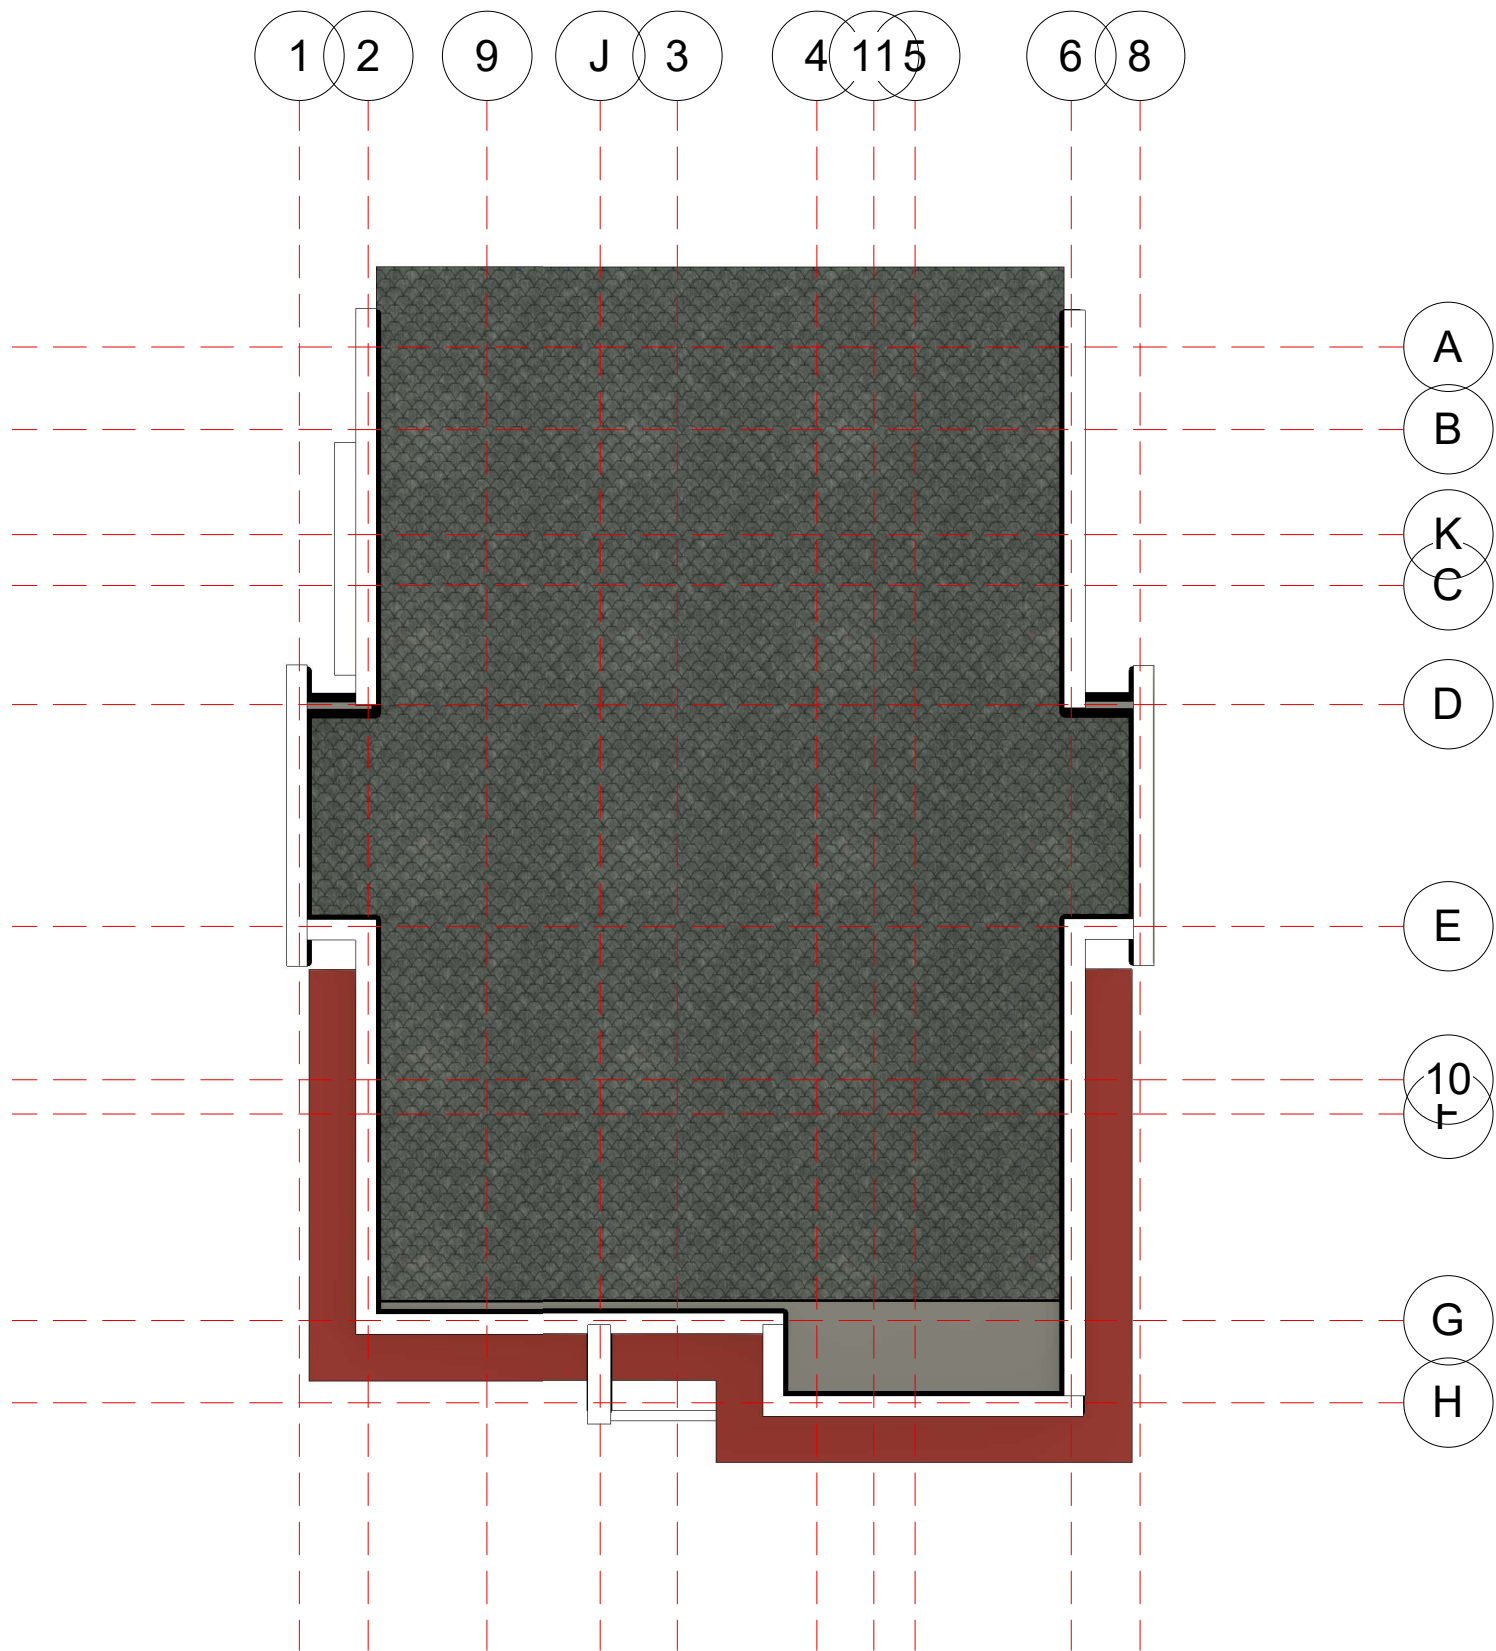

Notes:

Rev No..	Date	Description
----------	------	-------------

Revision No.

AFR/1175
RC:619405

SCYNA MATRIX LTD

ARCHITECTURE ENGINEERING CONSTRUCTION

B004, KADO MALL, AHMADU BELLO WAY, ABUJA, FCT

E-mail: scynamatrixltd@gmail.com

Tel: 08035951088, 09056554220

Project:
Project Name

Client:
Owner


Design by:
Designer

Drg. Title
ROOF PLAN

Date 07/29/22
Scale 1 : 100

Drg. No.

A103

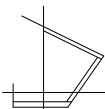

ELEVATIONS



FRONT ELEVATION



REAR ELEVATION

Notes:

Rev No..	Date	Description
----------	------	-------------

Revision No.

AFR/1175
RC:619405

SCYNA MATRIX LTD
ARCHITECTURE **ENGINEERING** CONSTRUCTION
B004, KADO MALL, AHMADU BELLO WAY, ABUJA, FCT
E-mail: scynamatrixltd@gmail.com
Tel: 08035951088, 09056554220

Project:
Project Name

Client:
Owner


Design by:
Designer

Drg. Title
ELEVATIONS

Date	03/30/23
Scale	1 : 120

Drg. No.

A105

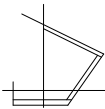

ELEVATION



RIGHT SIDE ELEVATION



LEFT SIDE ELEVATION

Notes:

Rev No..	Date	Description
----------	------	-------------

Revision No.

AFR/1175
RC:619405

SCYNA MATRIX LTD
ARCHITECTURE **ENGINEERING** CONSTRUCTION
B004, KADO MALL, AHMADU BELLO WAY, ABUJA, FCT
E-mail: scynamatrixltd@gmail.com
Tel: 08035951088, 09056554220

Project:

Project Name

Client:

Owner

Design by:

Designer

Drg. Title


ELEVATION

Date	03/30/23
------	----------


Scale	As indicated
-------	--------------

Drg. No.

A106

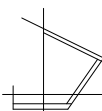


SECTION A-A

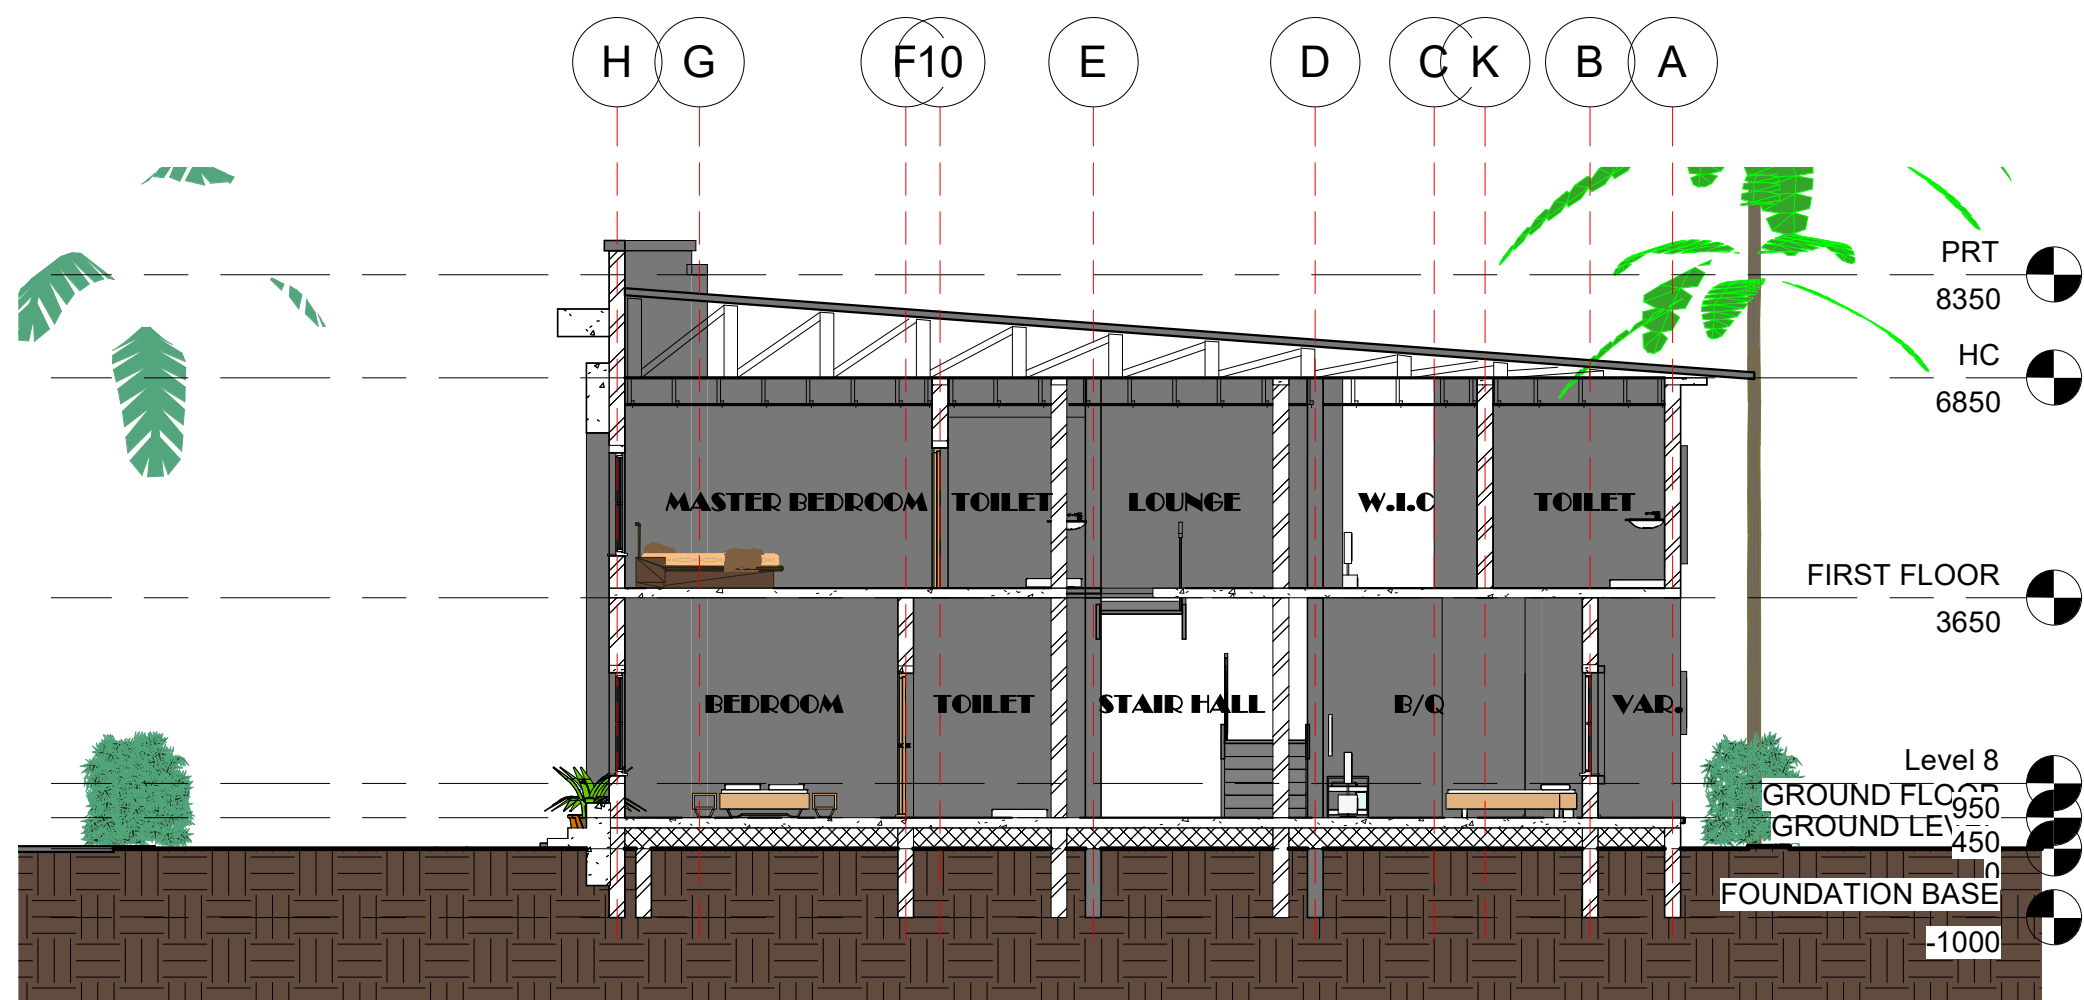

Notes:

Rev No.	Date	Description
Revision No.		
AFR/1175 RC:619405 SCYNA MATRIX LTD ARCHITECTURE ENGINEERING CONSTRUCTION B004, KADO MALL, AHMADU BELLO WAY, ABUJA, FCT E-mail: scynamatrixltd@gmail.com Tel: 08035951088, 09056554220		
Project: Project Name		
Client: Owner		
Design by: Designer		
Drg. Title SECTION A-A		
Date 03/30/23		
Scale 1 : 100		
Drg. No. A107		

SECTION B-B

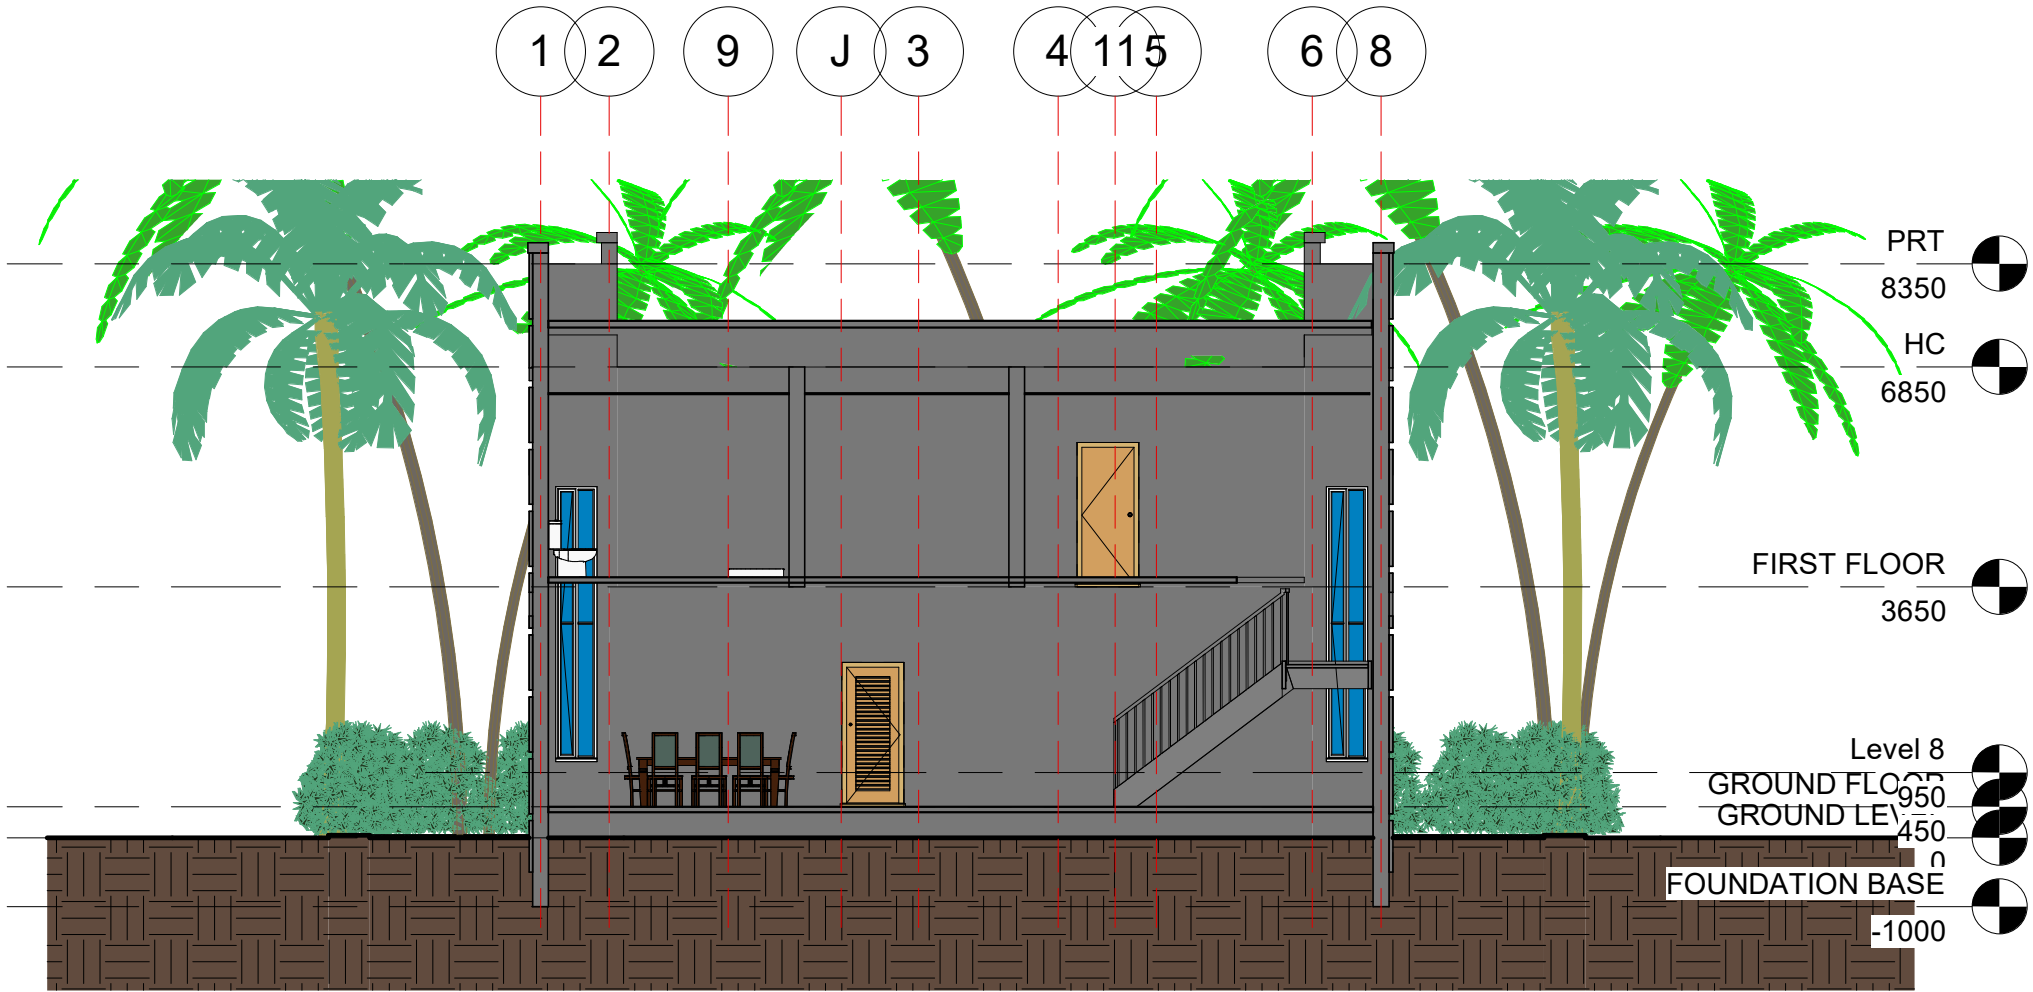

Notes:

Rev No.	Date	Description
---------	------	-------------

Revision No.

AFR/1175
RC:619405
SCYNA MATRIX LTD
ARCHITECTURE ENGINEERING CONSTRUCTION
B004, KADO MALL, AHMADU BELLO WAY, ABUJA, FCT
E-mail: scynamatrixltd@gmail.com
Tel: 08035951088, 09056554220

Project:

Project Name

Client:

Owner

Design by:

Designer

Drg. Title


SECTION B-B

Date **03/30/23**

Scale **1 : 100**

Drg. No.

A108

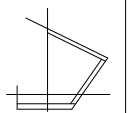

PERSPECTIVES



Notes:

Rev No..	Date	Description
----------	------	-------------

Revision No.

AFR/1175
RC:619405
SCYNA MATRIX LTD
ARCHITECTURE ENGINEERING CONSTRUCTION
B004, KADO MALL, AHMADU BELLO WAY, ABUJA,
FCT
E-mail: scynamatrixltd@gmail.com
Tel: 08035951088, 09056554220

Project:
Project Name

Client:
Owner

Design by:
Designer

Drg. Title
PERSPECTIVES

Date	03/30/23
Scale	As indicated

Drg. No.

A109

