

PROPOSED RESIDENTIAL DEVELOPMENT
AT
LP. KN 51
NO. 111, GIGINYU LG, KANO STATE.



ALH. ABDULMANAF YUNUSA



3-D VIEW

NOTES

SEAC
ARCHITECTS



No.	Description	Date

PROJECT NAME

PROPOSED RESIDENTIAL
DEVELOPMENT

PROJECT ADDRESS

LP. KN 51
NO. I-II, GIGINYU LG, KANO STATE.

CLIENT

ABDULMANAF YUNUSA

Designed By: ARC. Mustapha Shelu Usman

Checked by: Arc. Shelu Usman

Date: MARCH, 2024.

Contact: 08060092211

email: mskainuwa@gmail.com

Scale



3-D VIEW

NOTES		
SEAC ARCHITECTS		
		
		
No.	Description	Date
PROJECT NAME		
PROPOSED RESIDENTIAL DEVELOPMENT		
PROJECT ADDRESS		
I.P. KN 51 NO. I-II, GIGINYU LG, KANO STATE.		
CLIENT		
ABDULMANAF YUNUSA		
Designed By: ARC. Mustapha Shelu Usman		
Checked by: Arc. Shelu Usman		
Date: MARCH, 2024.		
Contact: 08060092211		
email: mskainuwa@gmail.com		
Scale		



3-D VIEW

NOTES

SEAC
ARCHITECTS



No.	Description	Date

PROJECT NAME

PROPOSED RESIDENTIAL
DEVELOPMENT

PROJECT ADDRESS

I.P. KN 51
NO. I-II, GIGINYU LG, KANO STATE.

CLIENT

ABDULMANAF YUNUSA

Designed By: ARC. Mustapha Shelu Usman

Checked by: Arc. Shelu Usman

Date: MARCH, 2024.

Contact: 08060092211

email: mskainuwa@gmail.com

Scale



3-D VIEW

NOTES

SEAC
ARCHITECTS



No.	Description	Date

PROJECT NAME

PROPOSED RESIDENTIAL
DEVELOPMENT

PROJECT ADDRESS

LP. KN 51
NO. I-II, GIGINYU LG, KANO STATE.

CLIENT

ABDULMANAF YUNUSA

Designed By: ARC. Mustapha Shelu Usman


Checked by: Arc. Shelu Usman

Date: MARCH, 2024.

Contact: 08060092211

email: mskainuwa@gmail.com

Scale

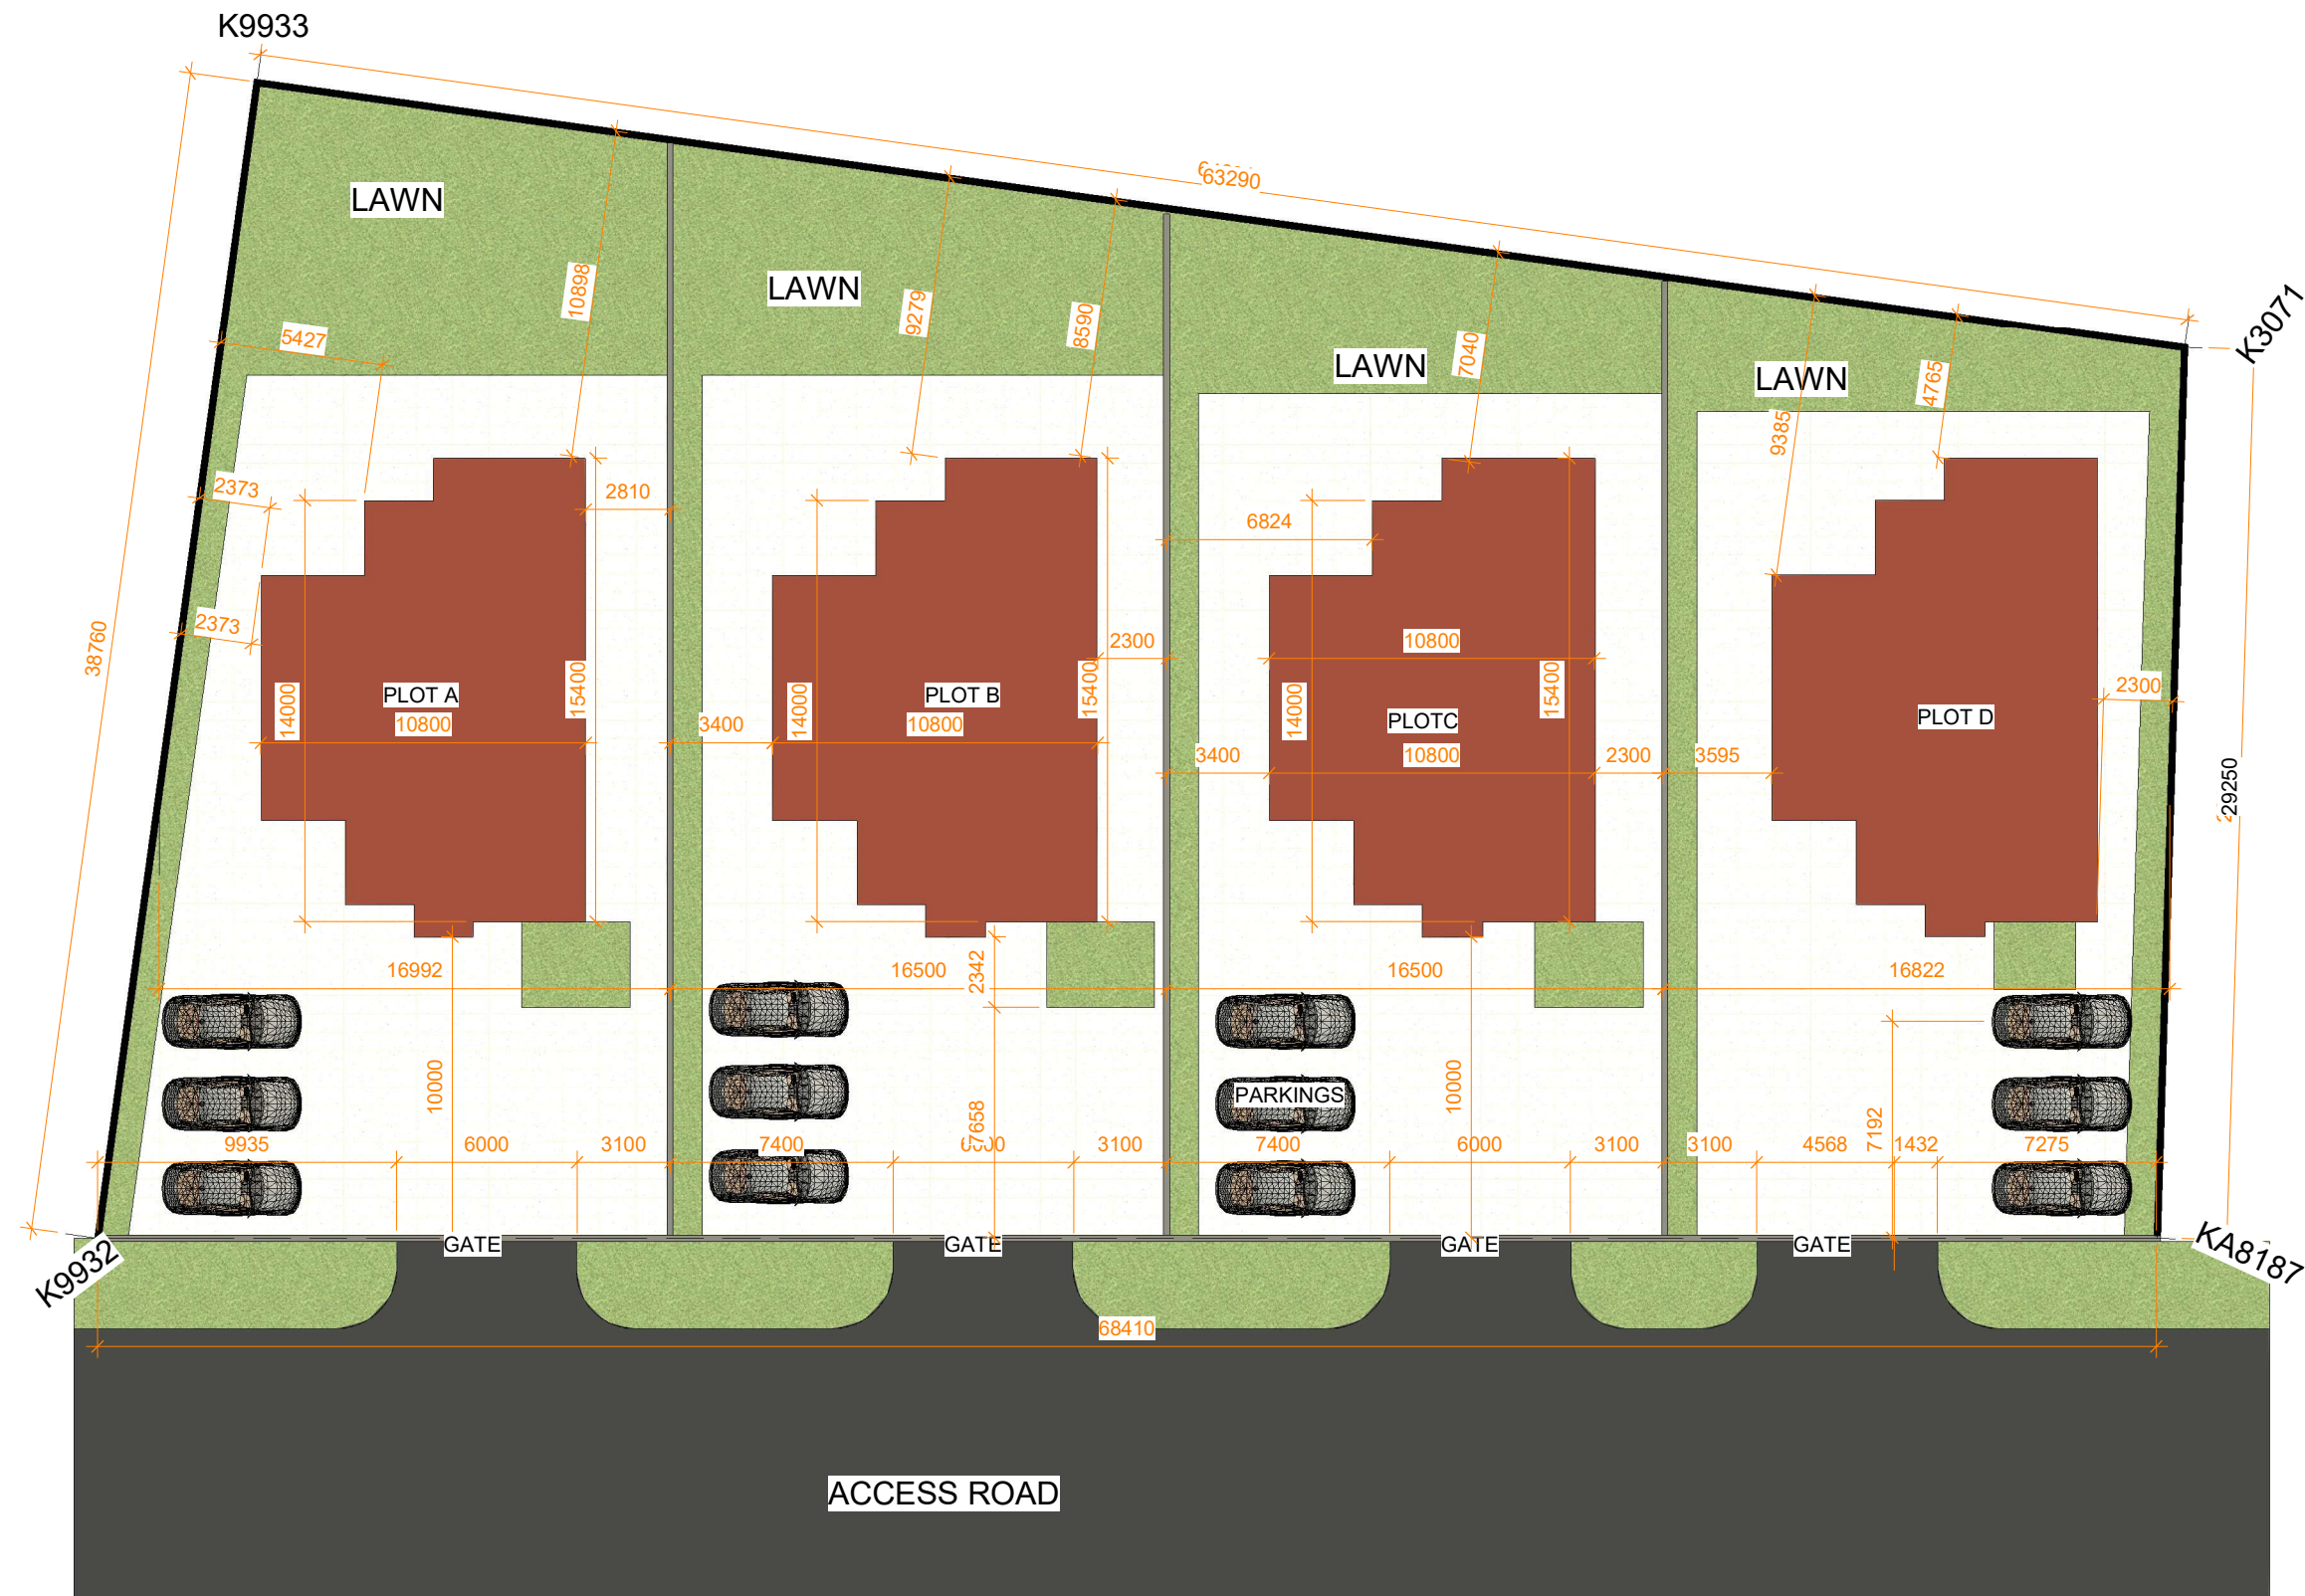

1 SITE-PLAN
1 : 125

NOTES

SEAC ARCHITECTS



No.	Description	Date

PROJECT NAME

PROPOSED RESIDENTIAL
DEVELOPMENT

PROJECT ADDRESS

LP. KN 51
NO. I-II, GIGINYU LG, KANO STATE.

CLIENT

ABDULMANAF YUNUSA

Designed By: ARC. Mustapha Shelu Usman

Checked by: Arc. Shelu Usman


Date: MARCH, 2024.

Contact: 08060092211

email: mskainuwa@gmail.com

Scale

1 : 125

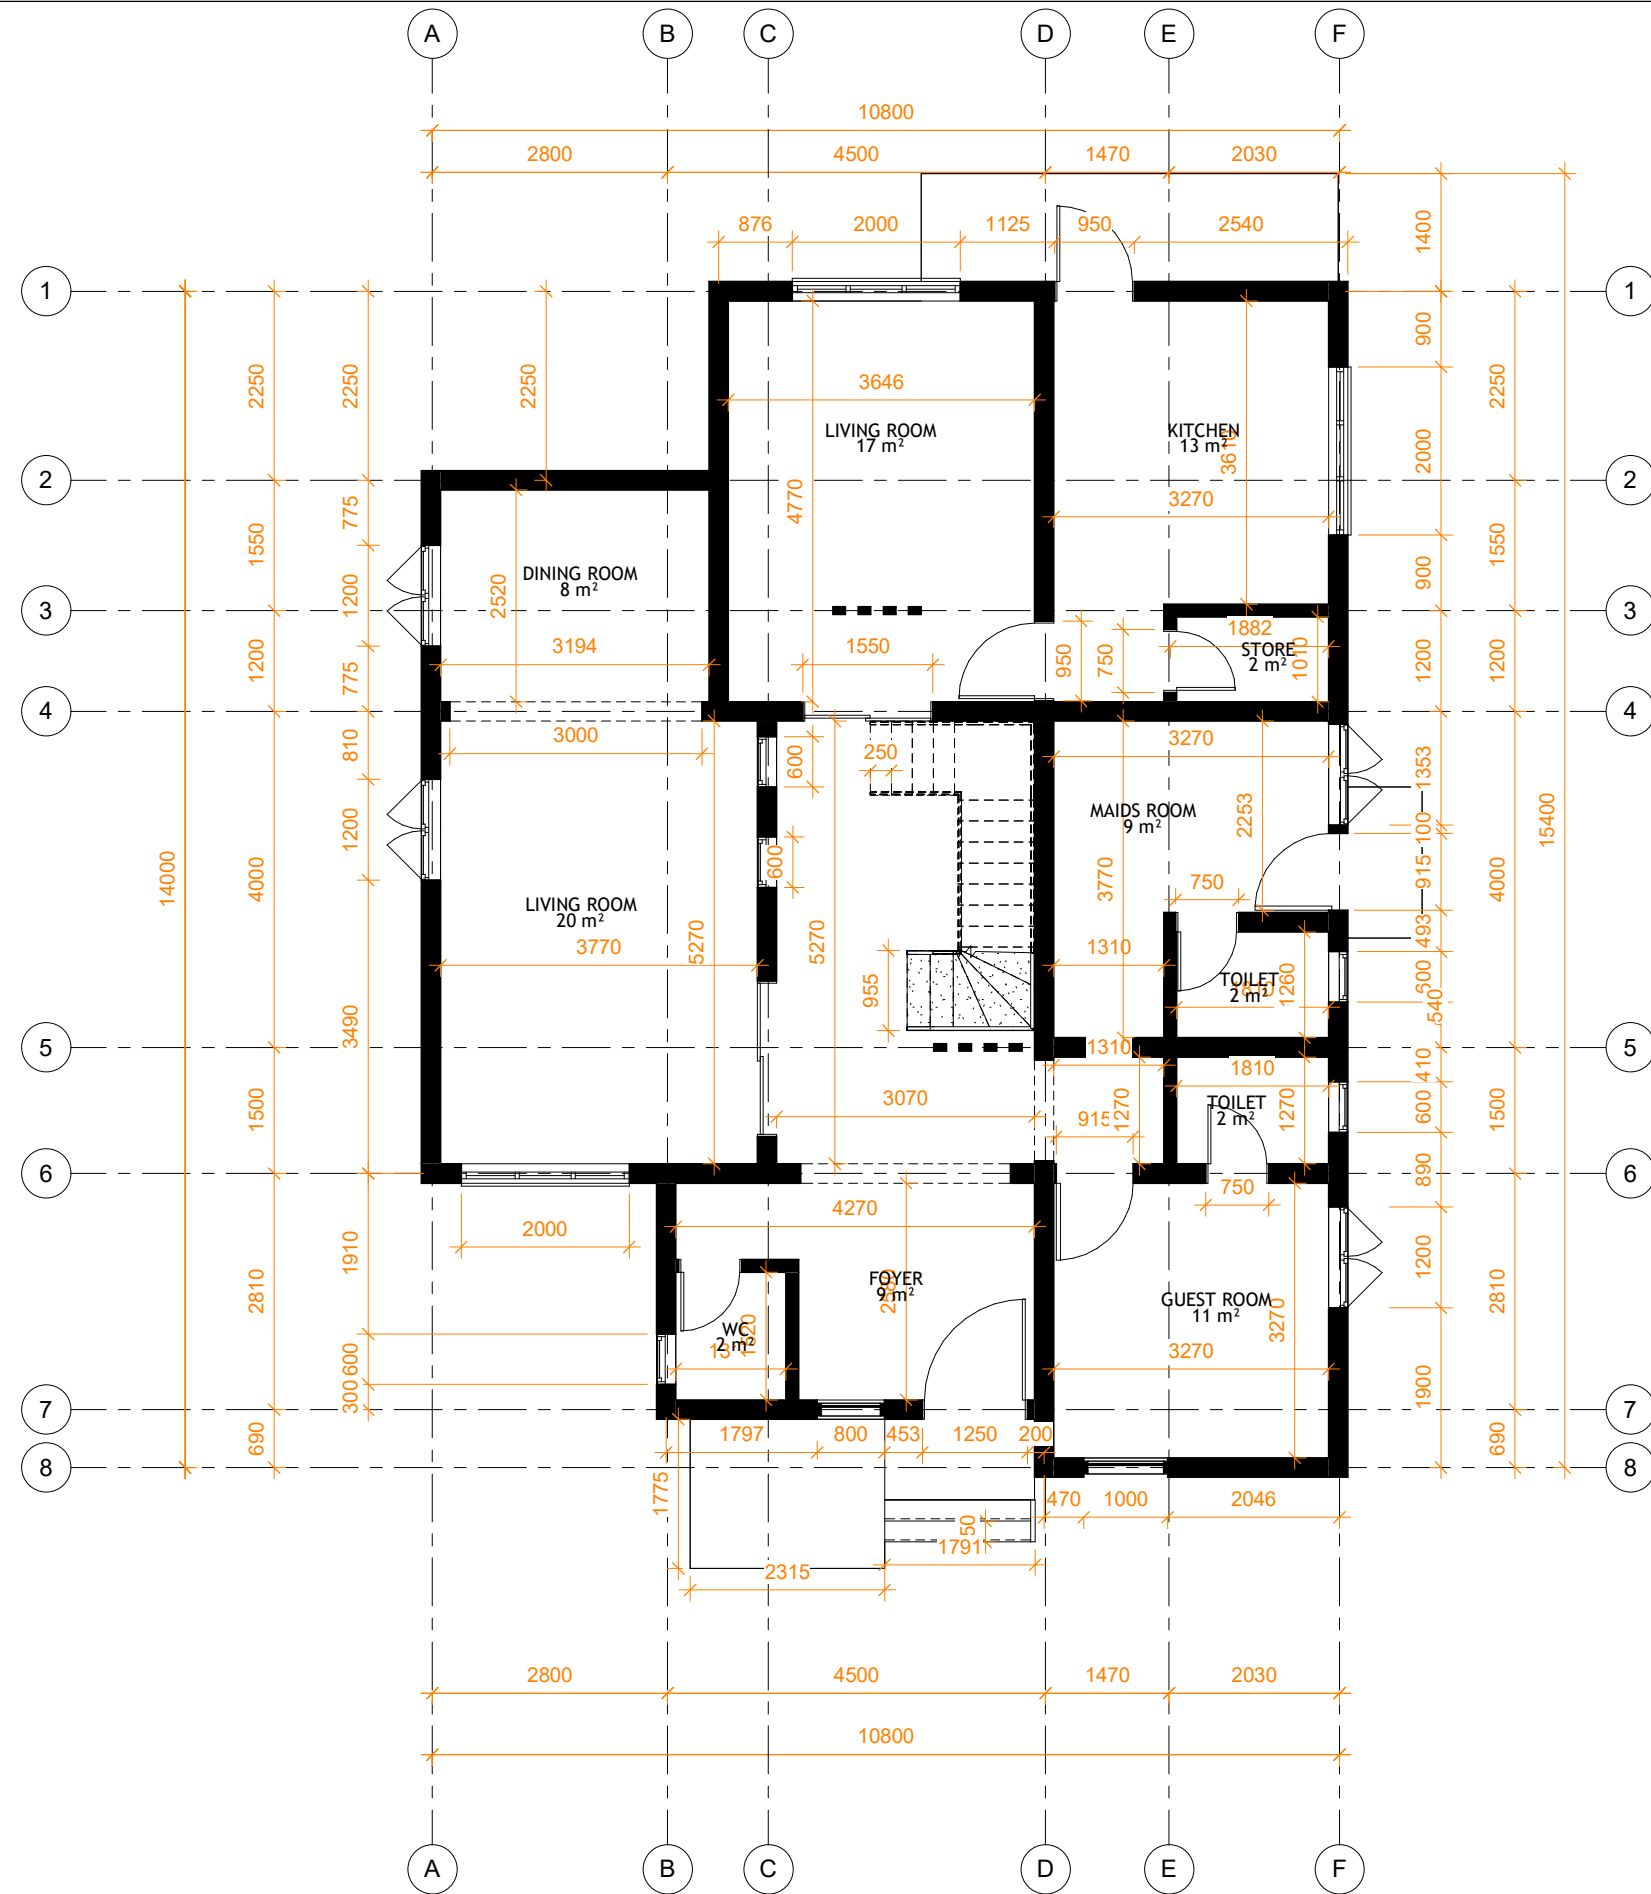

1 GROUND FLOOR PLAN
1 : 45

NOTES

SEAC ARCHITECTS



No.	Description	Date

PROJECT NAME

PROPOSED RESIDENTIAL
DEVELOPMENT

PROJECT ADDRESS

LP. KN 51
NO. I-II, GIGINYU LG, KANO STATE.

CLIENT

ABDULMANAF YUNUSA

Designed By: ARC. Mustapha Shelu Usman

Checked by: Arc. Shelu Usman


Date: MARCH, 2024.

Contact: 08060092211

email: mskainuwa@gmail.com

Scale

1 : 45

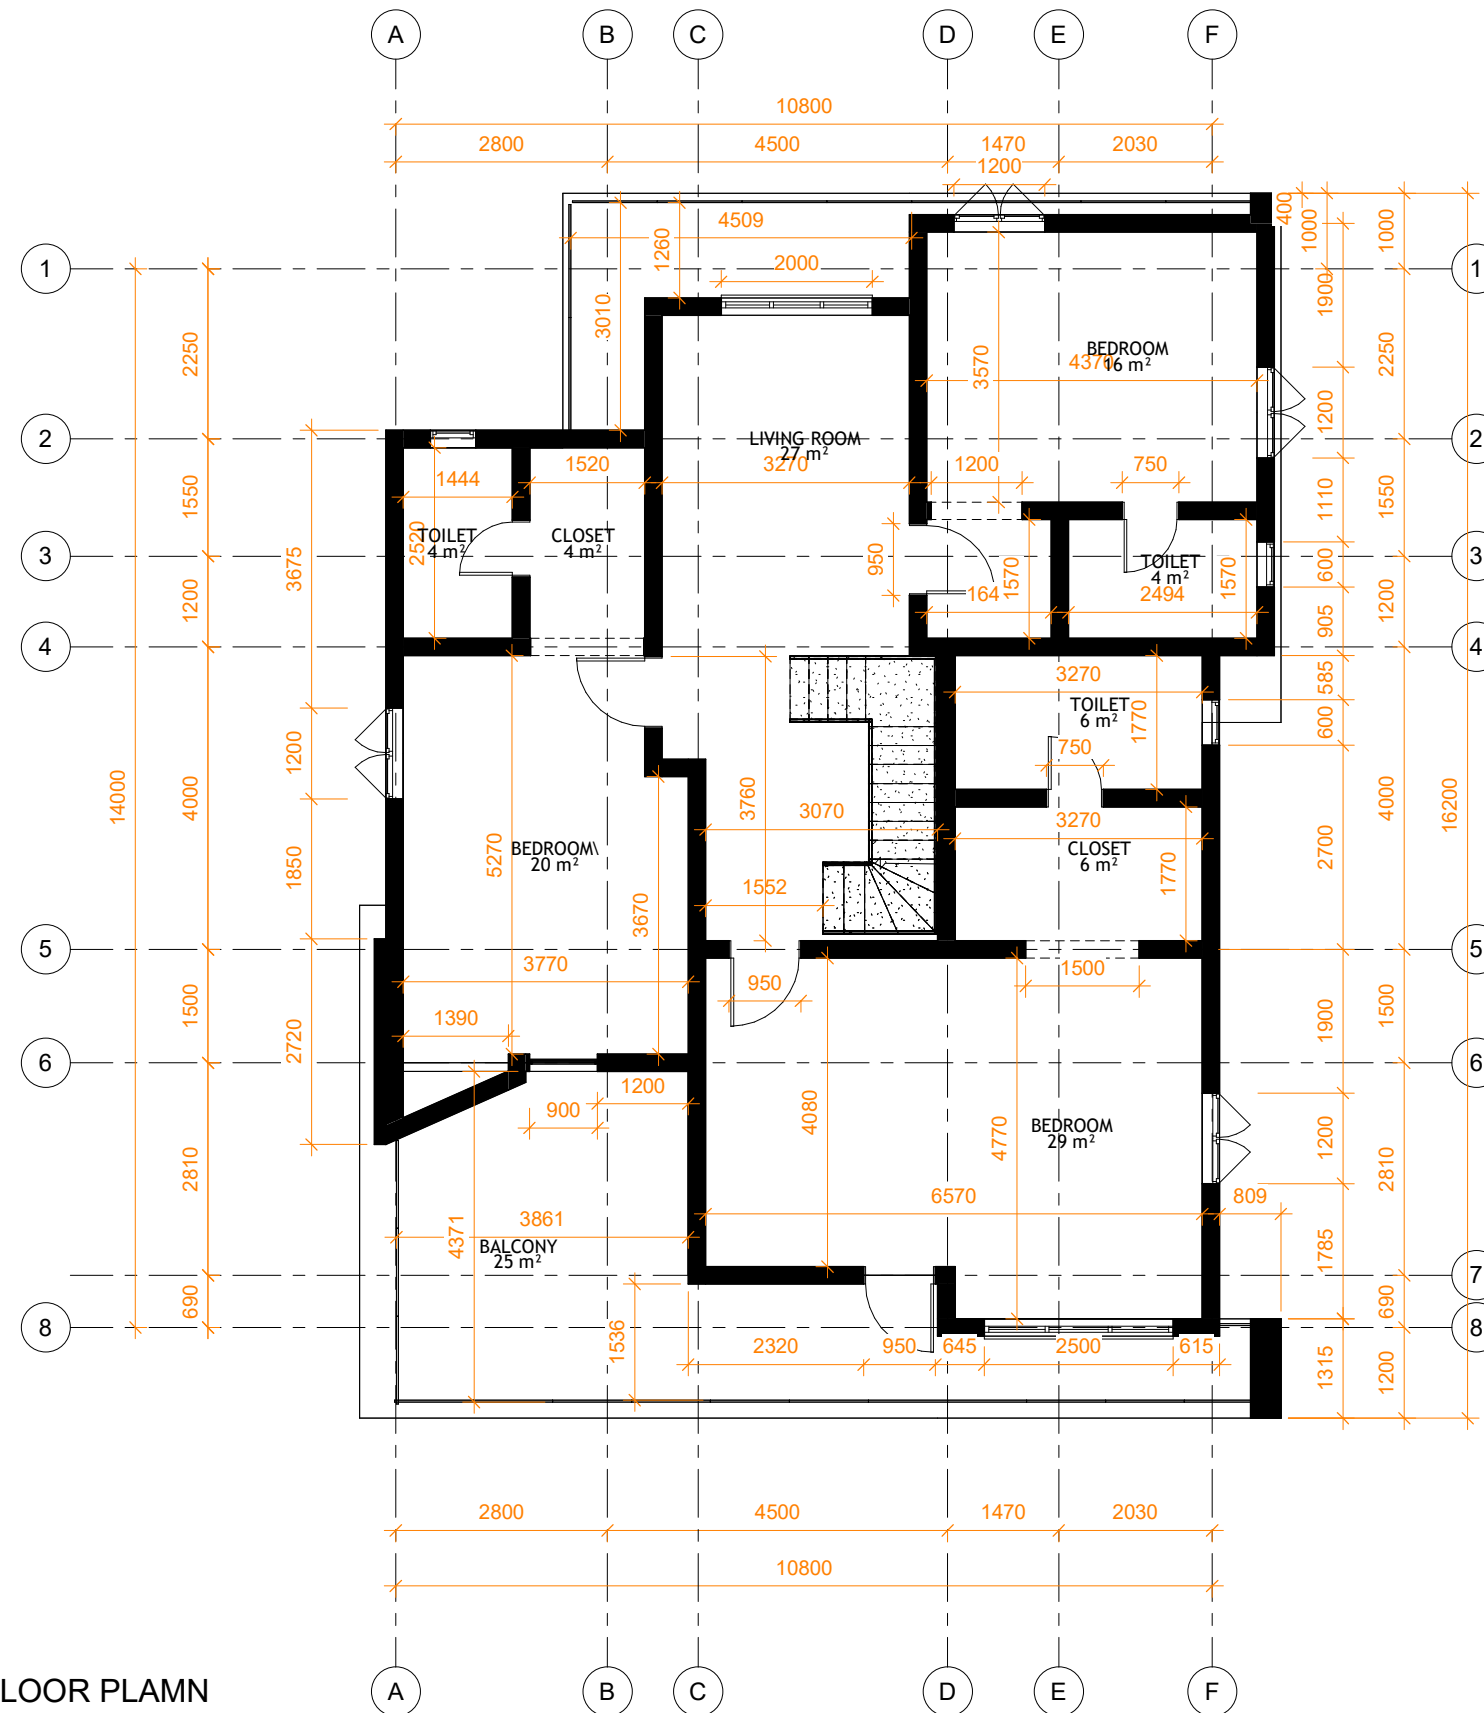

1 FIRST FLOOR PLAMN
1 : 50

NOTES

SEAC ARCHITECTS



No.	Description	Date

PROJECT NAME

PROPOSED RESIDENTIAL
DEVELOPMENT

PROJECT ADDRESS

LP. KN 51
NO. I-II, GIGINYU LG, KANO STATE.

CLIENT

ABDULMANAF YUNUSA

Designed By: ARC. Mustapha Shelu Usman


Checked by: Arc. Shelu Usman

Date: MARCH, 2024.

Contact: 08060092211

email: mskainuwa@gmail.com

Scale 1 : 50

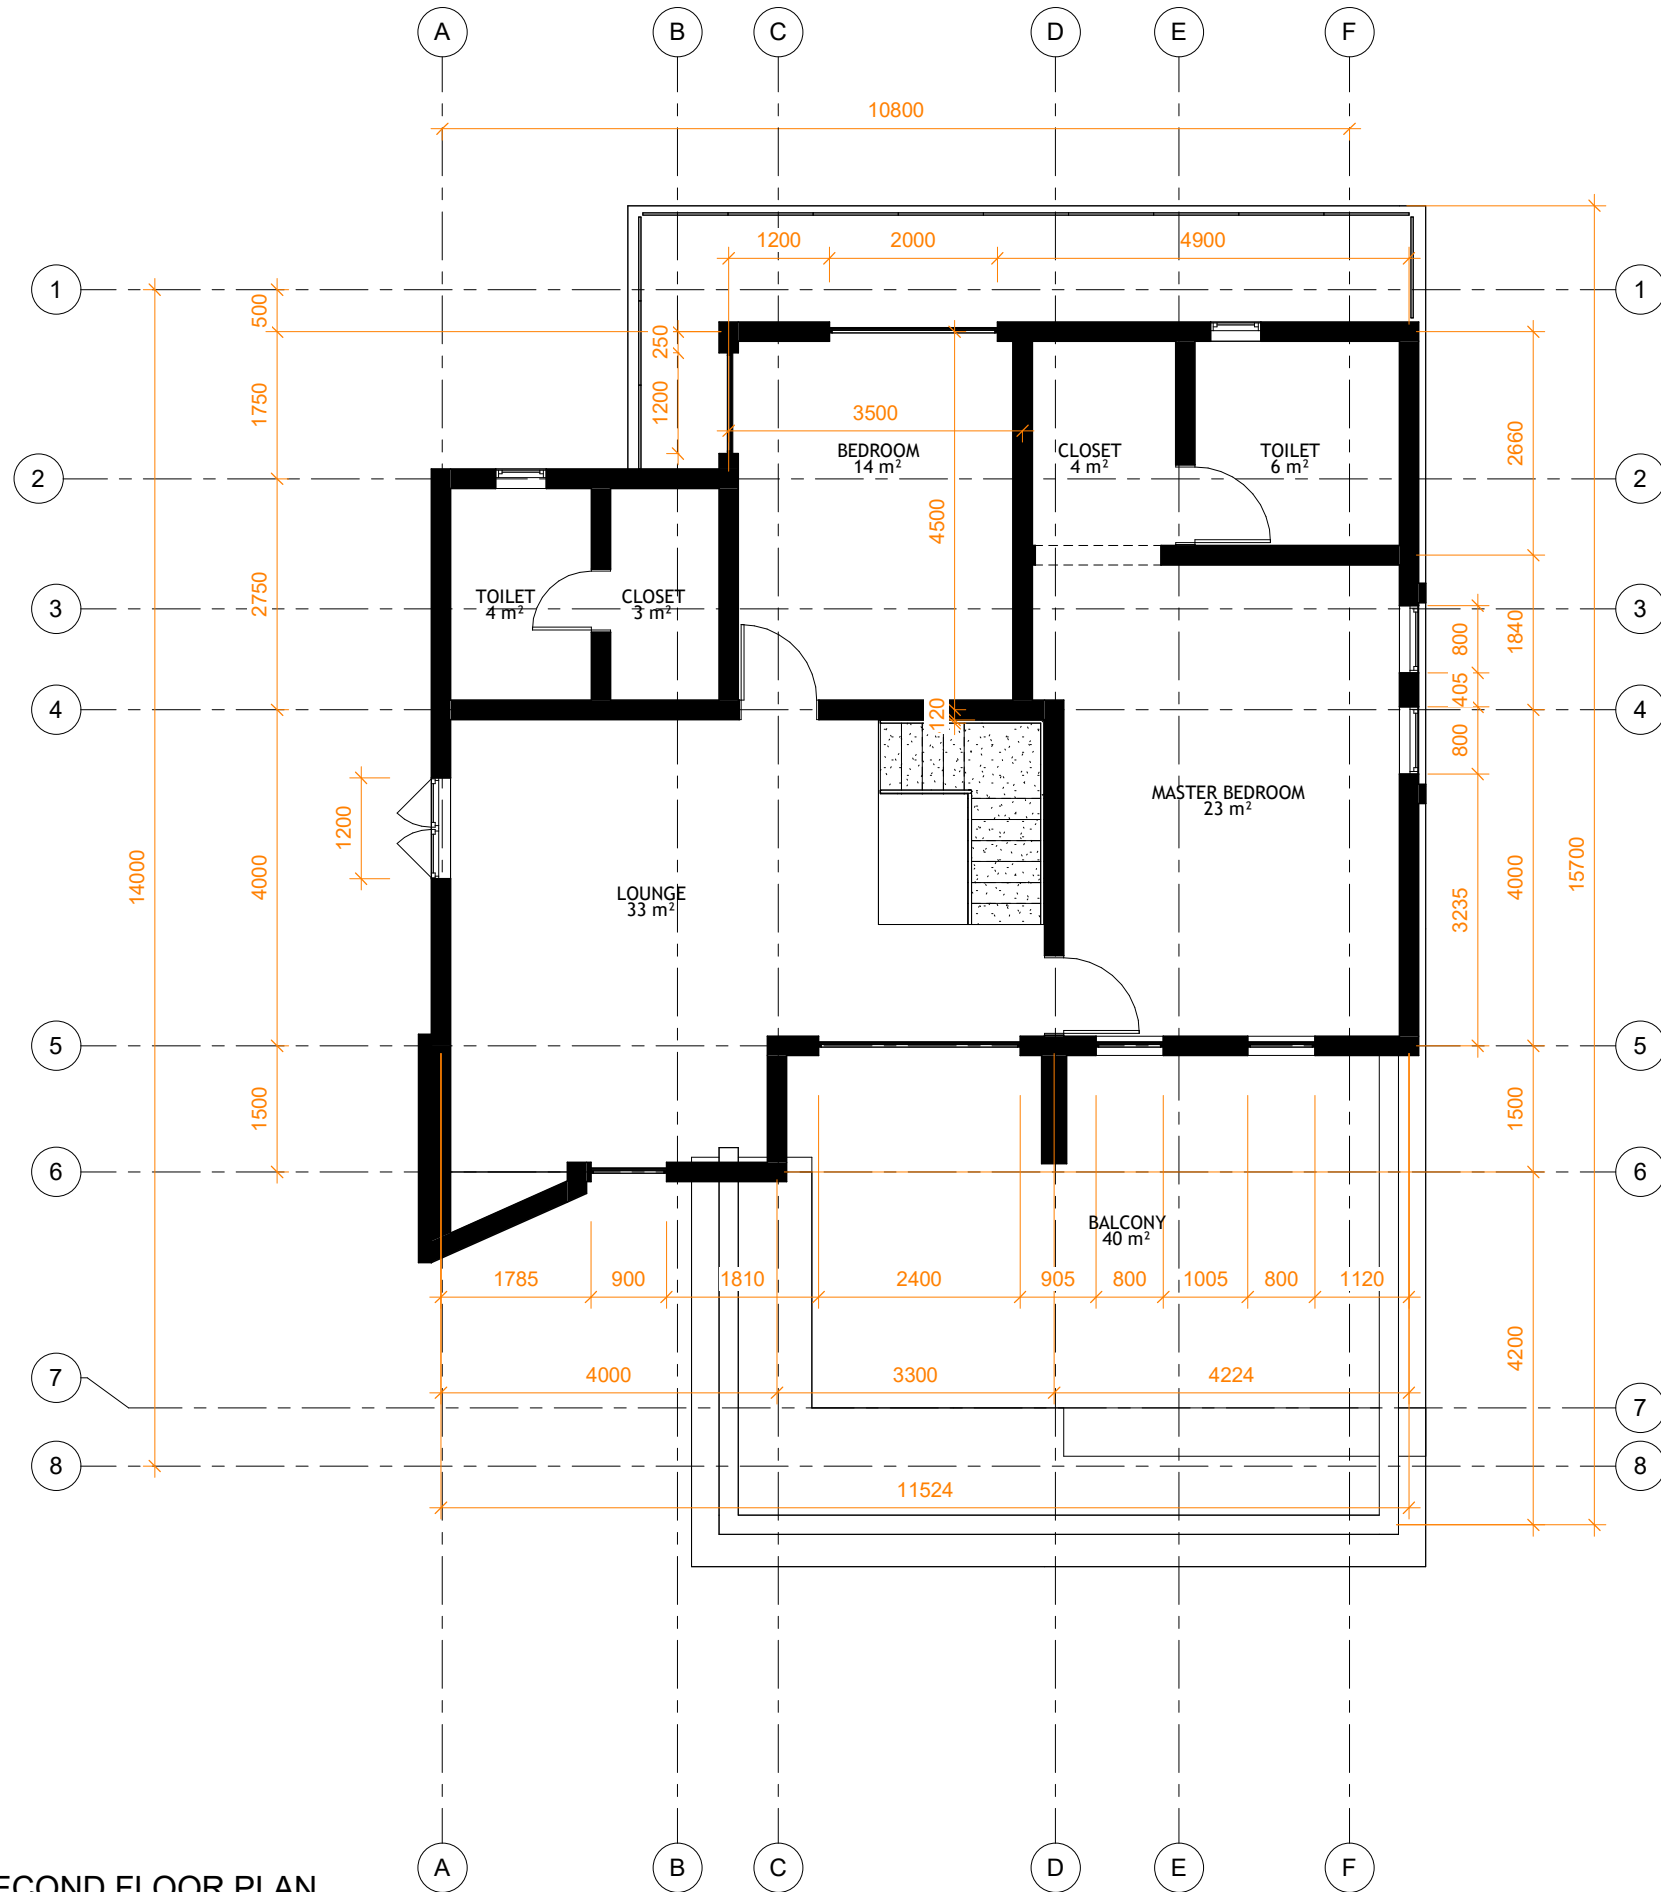

1 SECOND FLOOR PLAN
1 : 45

NOTES

SEAC
ARCHITECTS



No.	Description	Date

PROJECT NAME

PROPOSED RESIDENTIAL
DEVELOPMENT

PROJECT ADDRESS

LP. KN 51
NO. I-II, GIGINYU LG, KANO STATE.

CLIENT

ABDULMANAF YUNUSA

Designed By: ARC. Mustapha Shelu Usman


Checked by: Arc. Shelu Usman

Date: MARCH, 2024.

Contact: 08060092211

email: mskainuwa@gmail.com

Scale 1 : 45

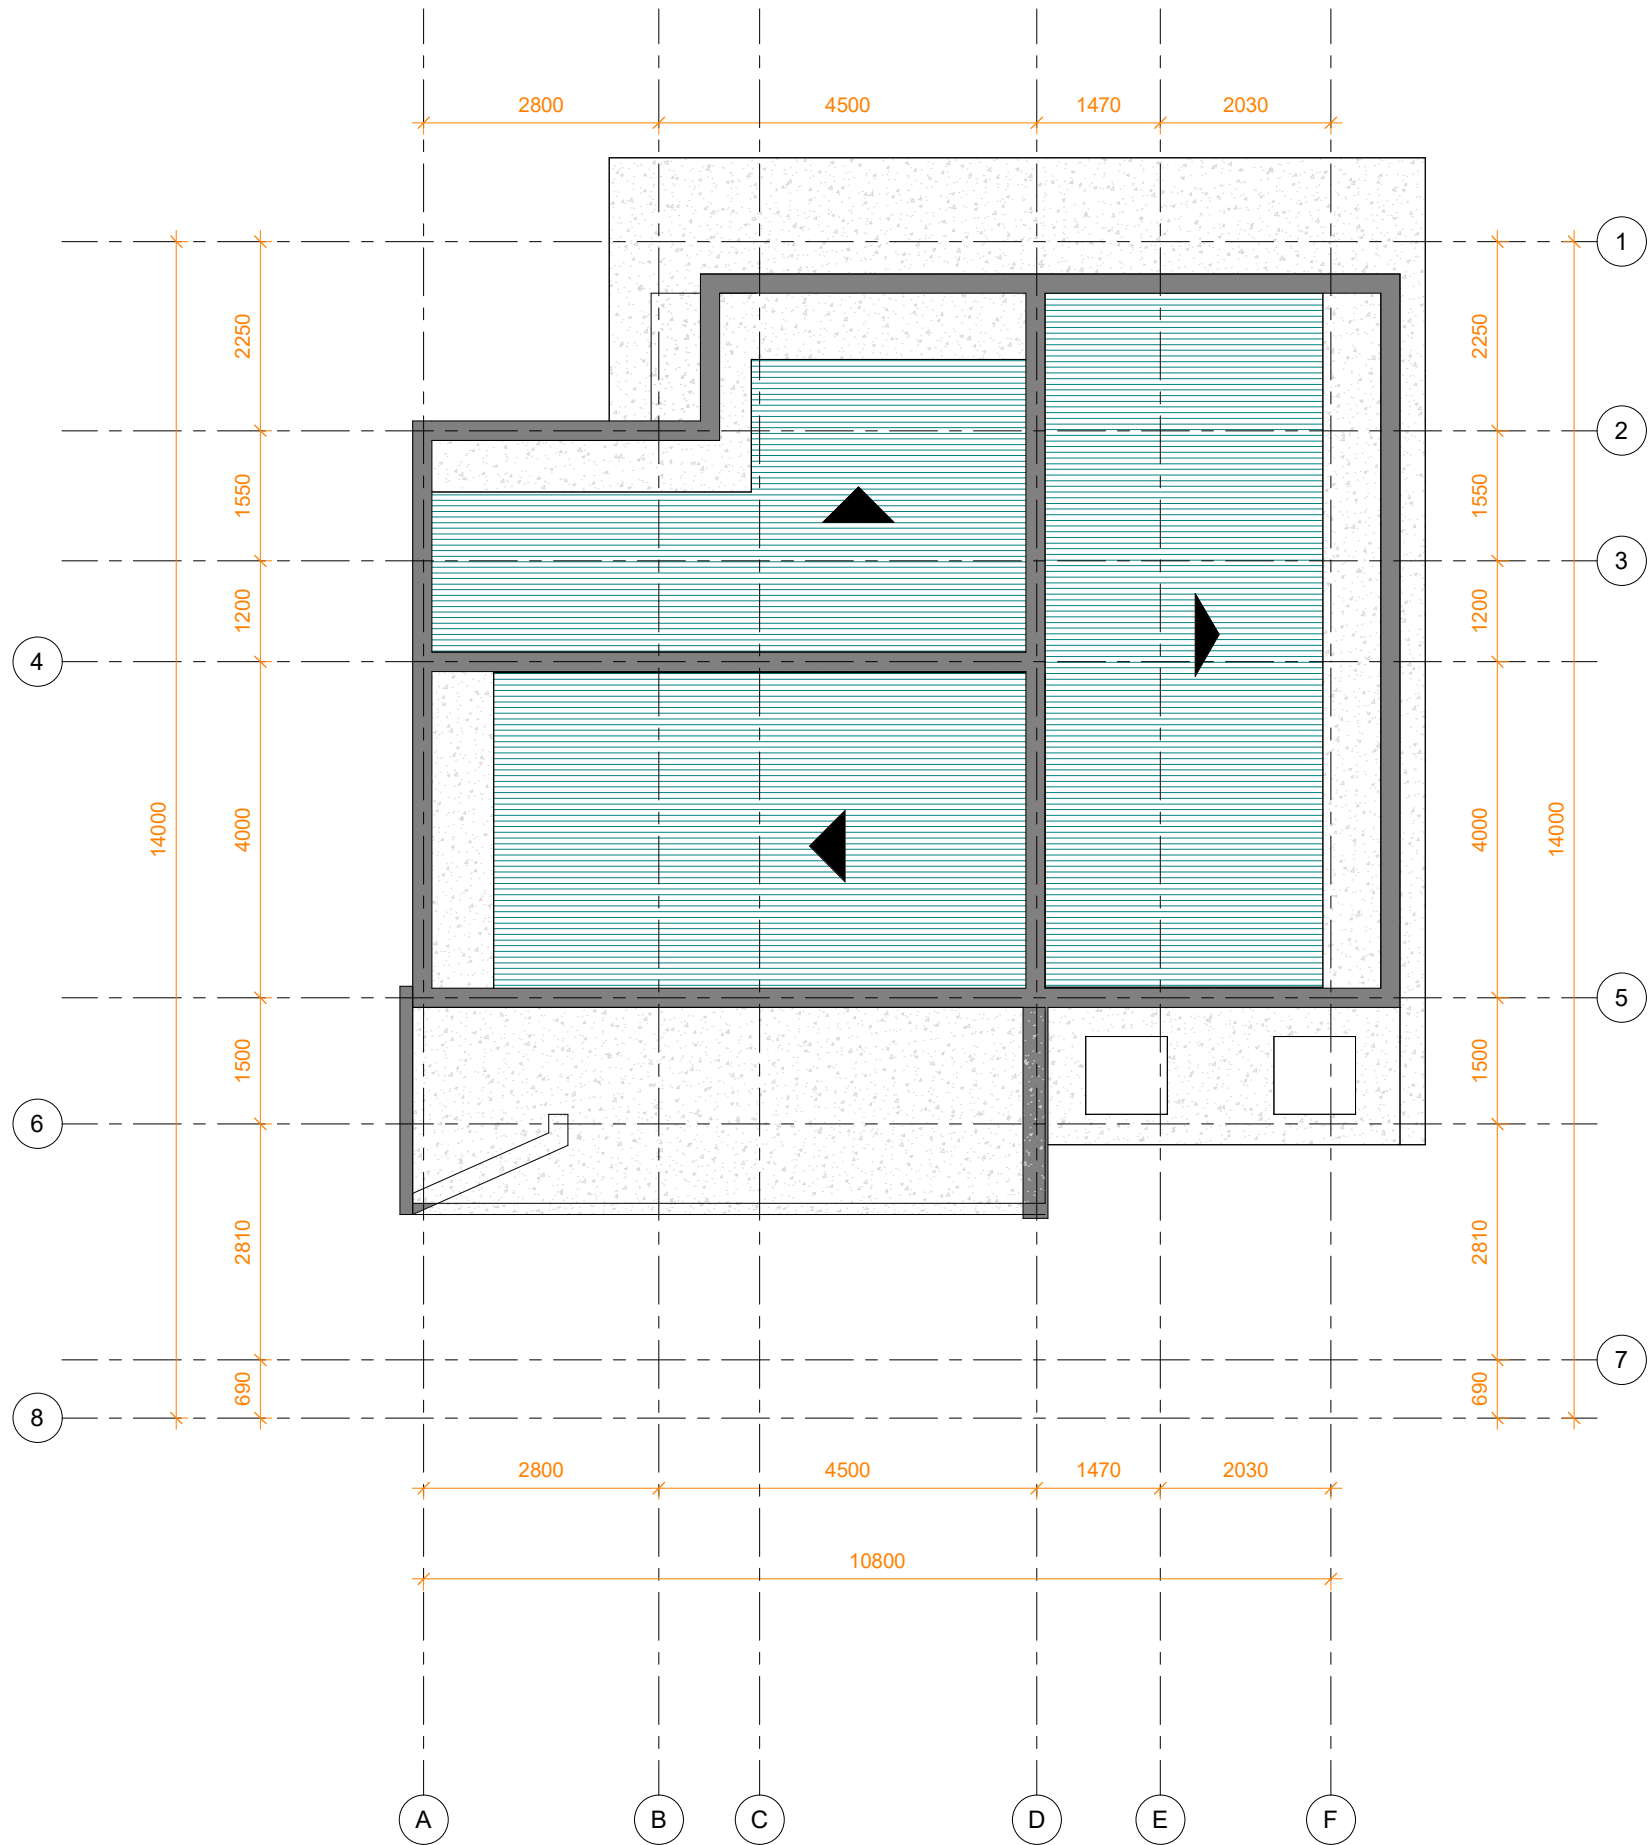

1 Level 5
1 : 45

NOTES

SEAC
ARCHITECTS



No.	Description	Date

PROJECT NAME

PROPOSED RESIDENTIAL
DEVELOPMENT

PROJECT ADDRESS

LP. KN 51
NO. I-II, GIGINYU LG, KANO STATE.

CLIENT

ABDULMANAF YUNUSA

Designed By: ARC. Mustapha Shehu Usman


Checked by: Arc. Shehu Usman

Date: MARCH, 2024.

Contact: 08060092211

email: mskainuwa@gmail.com

Scale 1 : 45

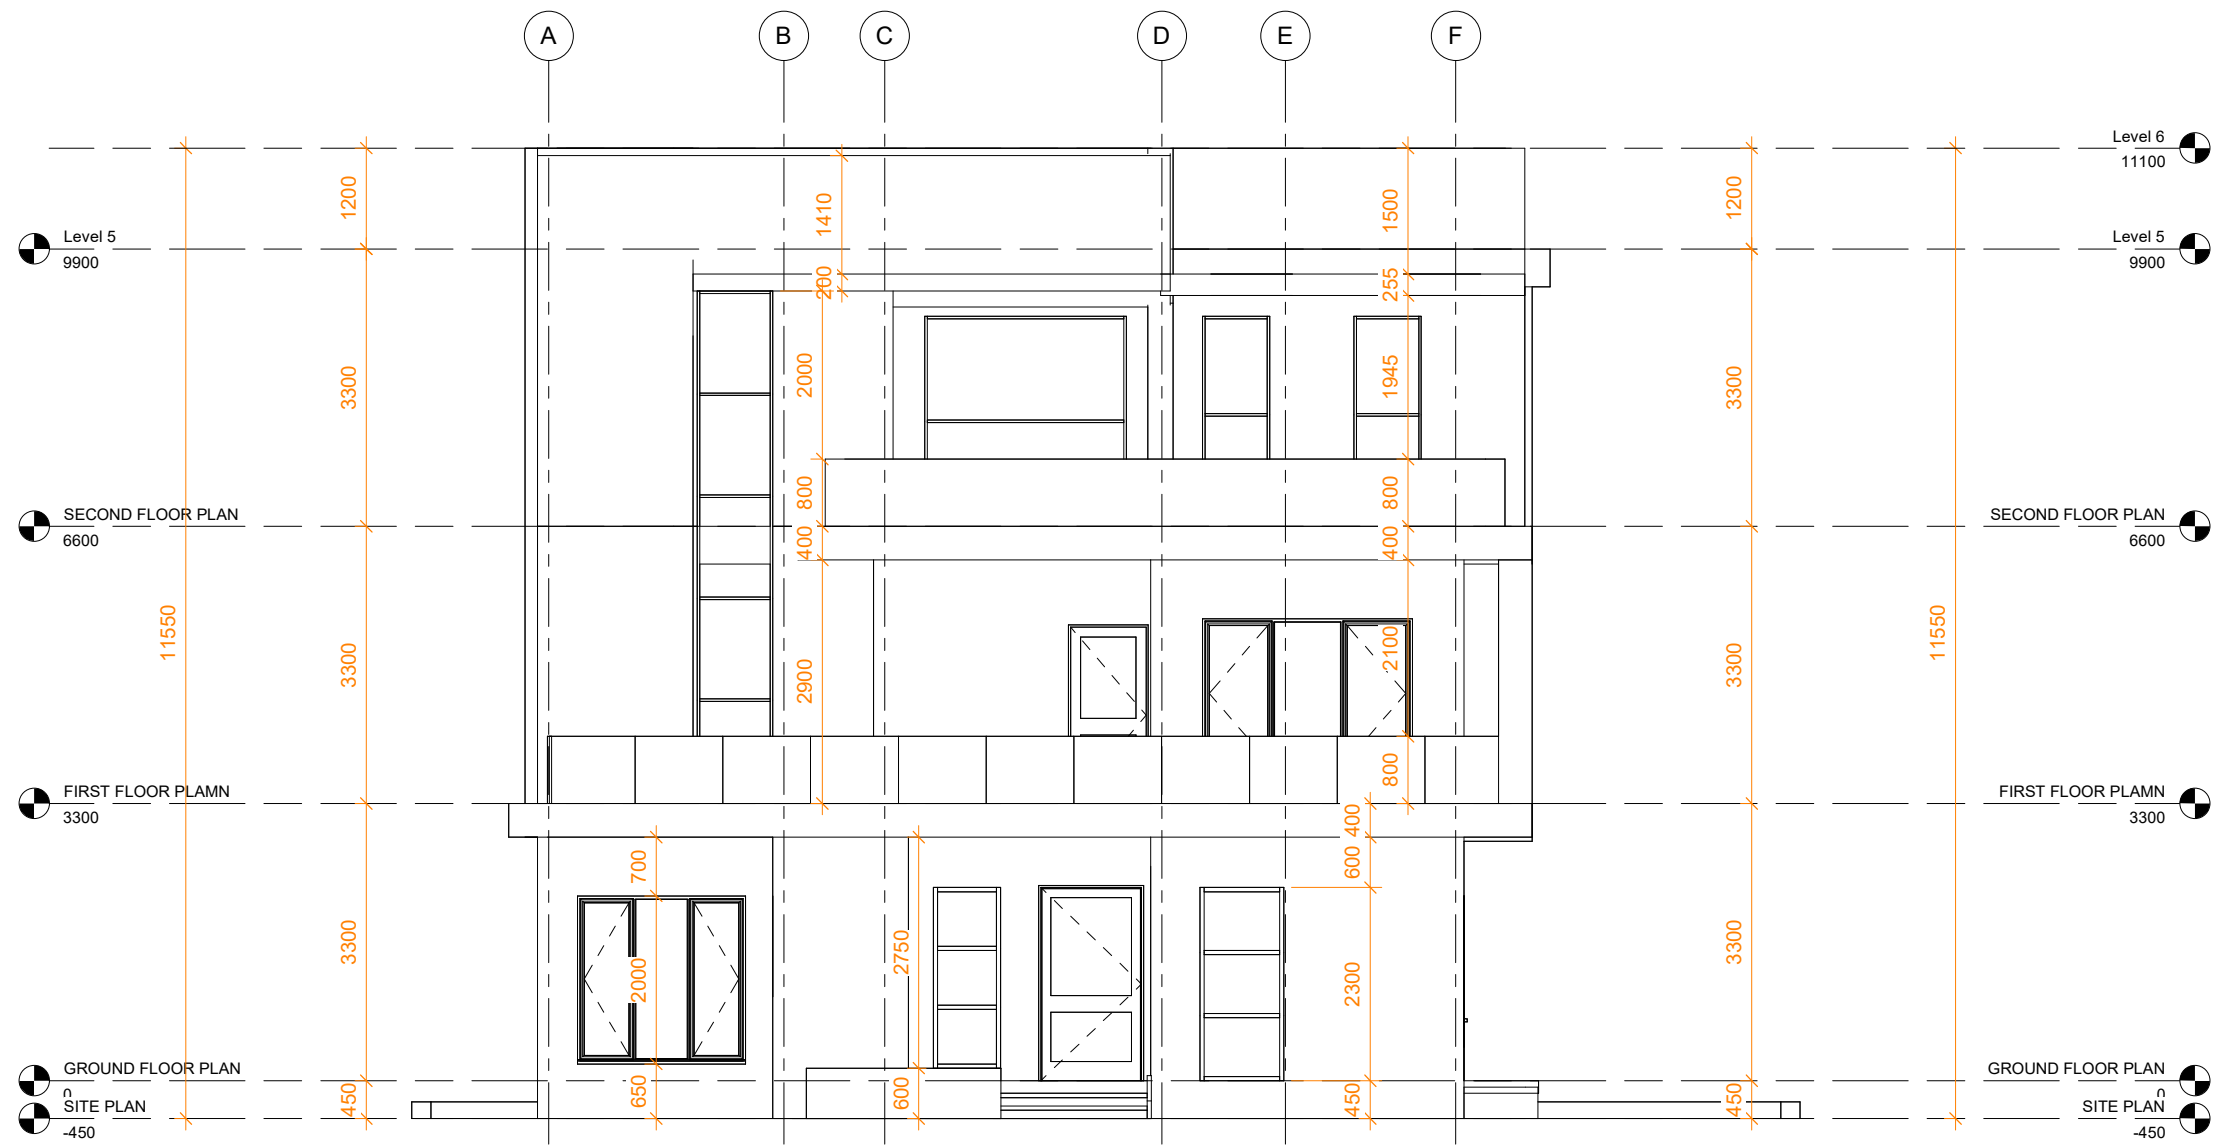

1 FRONT ELEVATION
1 : 45

NOTES

SEAC ARCHITECTS



No.	Description	Date

PROJECT NAME

PROPOSED RESIDENTIAL
DEVELOPMENT

PROJECT ADDRESS

I.P. KN 51
NO. I-II, GIGINYU LG, KANO STATE.

CLIENT

ABDULMANAF YUNUSA

Designed By: ARC. Mustapha Shehu Usman

Checked by: Arc. Shehu Usman


Date: MARCH, 2024.

Contact: 08060092211

email: mskainuwa@gmail.com

Scale

1 : 45

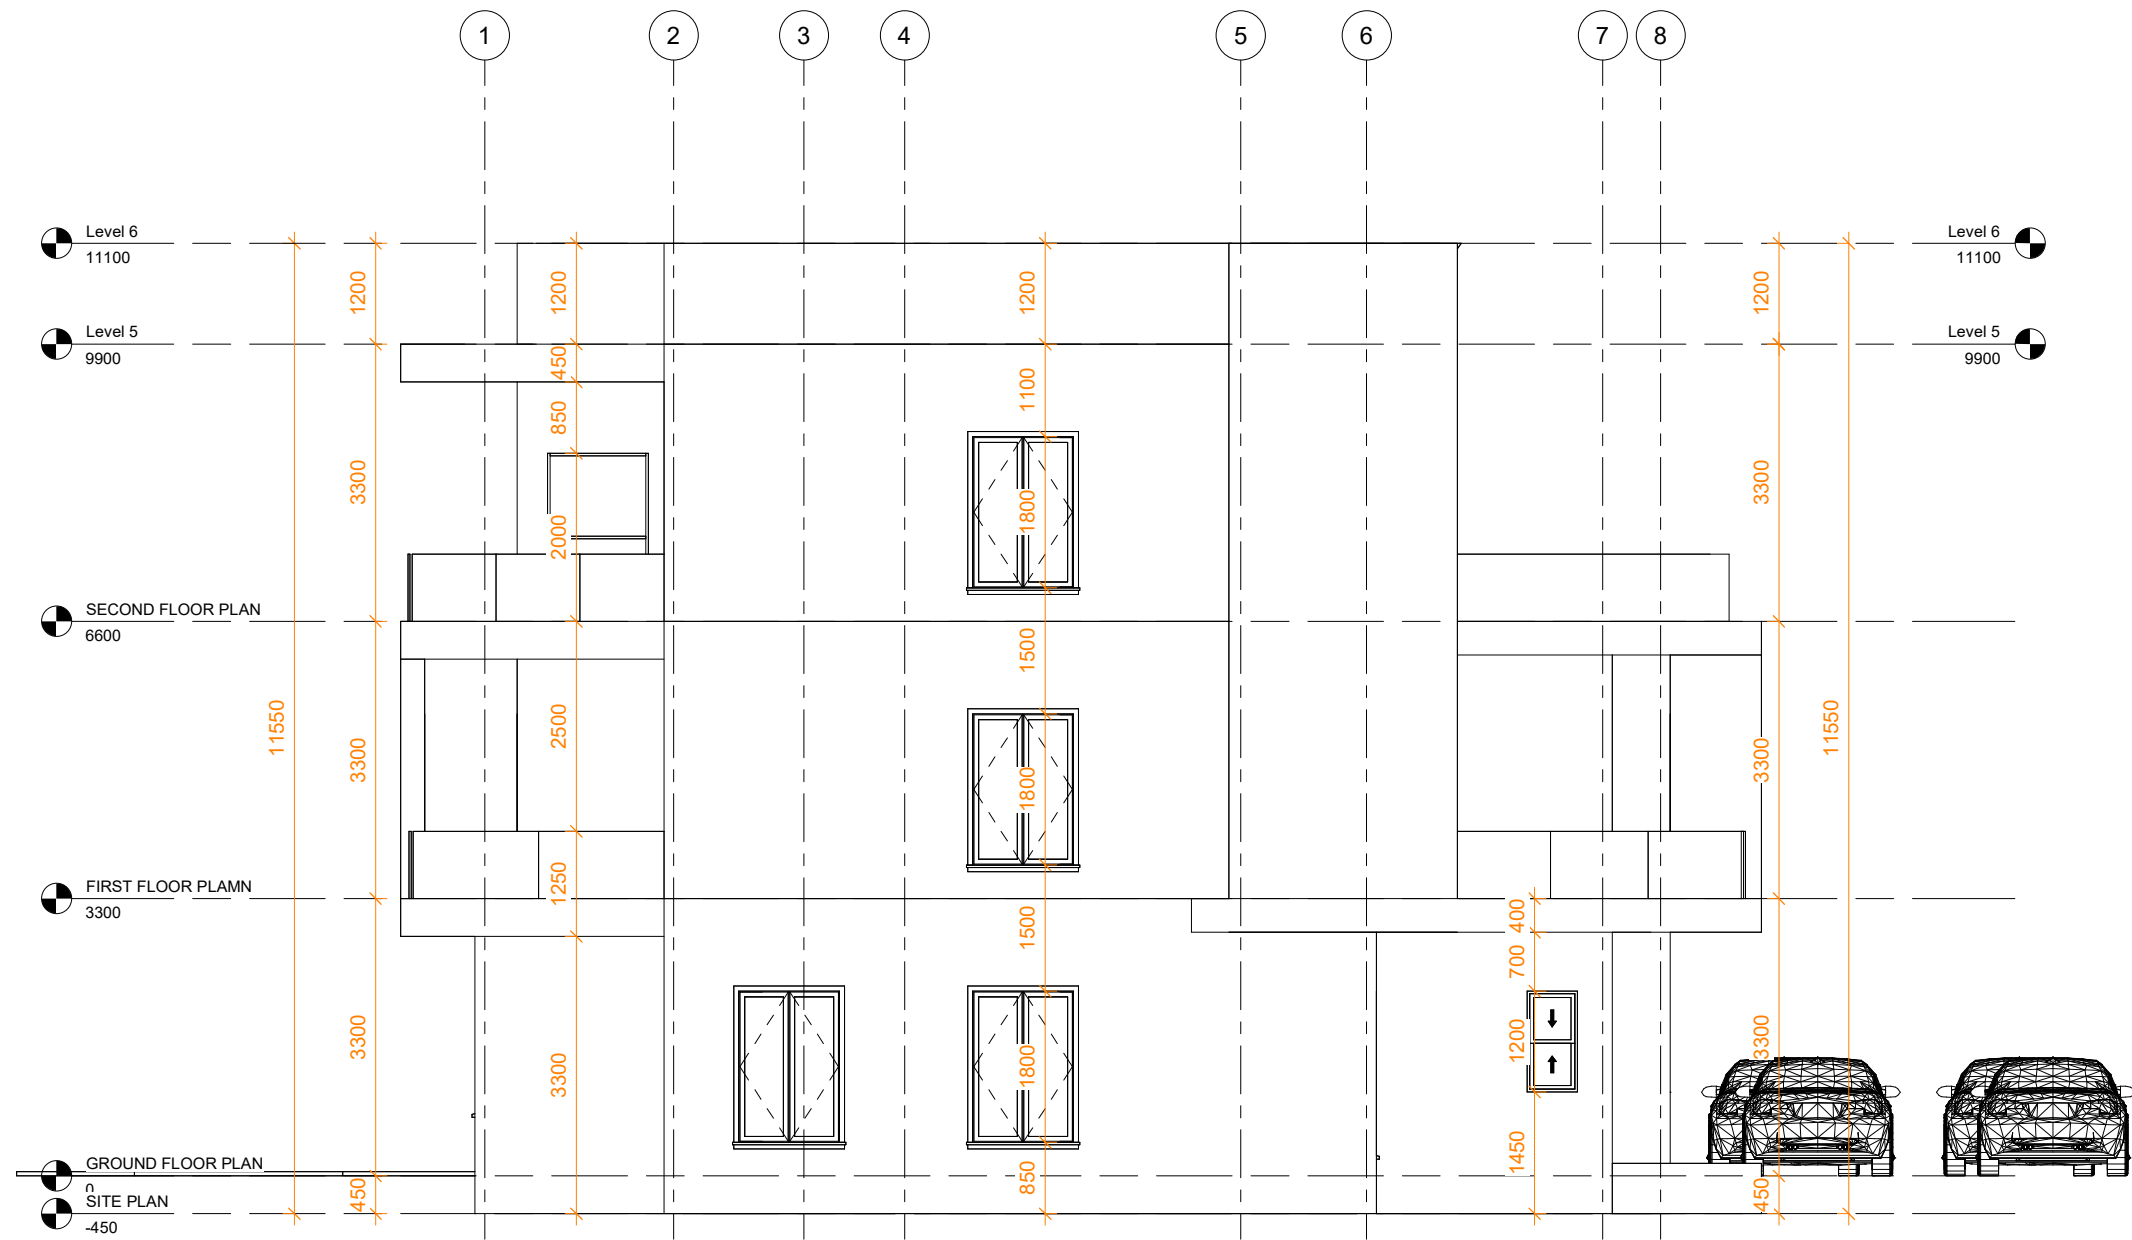

1 LEFT ELEVATION
1 : 45

NOTES

SEAC ARCHITECTS



No.	Description	Date

PROJECT NAME

PROPOSED RESIDENTIAL
DEVELOPMENT

PROJECT ADDRESS

LP. KN 51
NO. I-II, GIGINYU LG, KANO STATE.

CLIENT

ABDULMANAF YUNUSA

Designed By: ARC. Mustapha Shelu Usman

Checked by: Arc. Shelu Usman

Date: MARCH, 2024.

Contact: 08060092211

email: mskainuwa@gmail.com

Scale

1 : 45

NOTES

SEAC
ARCHITECTS



No.	Description	Date

PROJECT NAME

PROPOSED RESIDENTIAL
DEVELOPMENT

PROJECT ADDRESS

LP. KN 51
NO. I-II, GIGINYU LG, KANO STATE.

CLIENT

ABDULMANAF YUNUSA

Designed By: ARC. Mustapha Shelu Usman

Checked by: Arc. Shelu Usman

Date: MARCH, 2024.

Contact: 08060092211

email: mskainuwa@gmail.com

Scale 1 : 40



1 RIGHT ELEVATION
1 : 40

NOTES

SEAC
ARCHITECTS



No.	Description	Date

PROJECT NAME

PROPOSED RESIDENTIAL
DEVELOPMENT

PROJECT ADDRESS

LP. KN 51
NO. I-II, GIGINYU LG, KANO STATE.

CLIENT

ABDULMANAF YUNUSA

Designed By: ARC. Mustapha Shelu Usman


Checked by: Arc. Shelu Usman

Date: MARCH, 2024.

Contact: 08060092211

email: mskainuwa@gmail.com

Scale 1 : 45

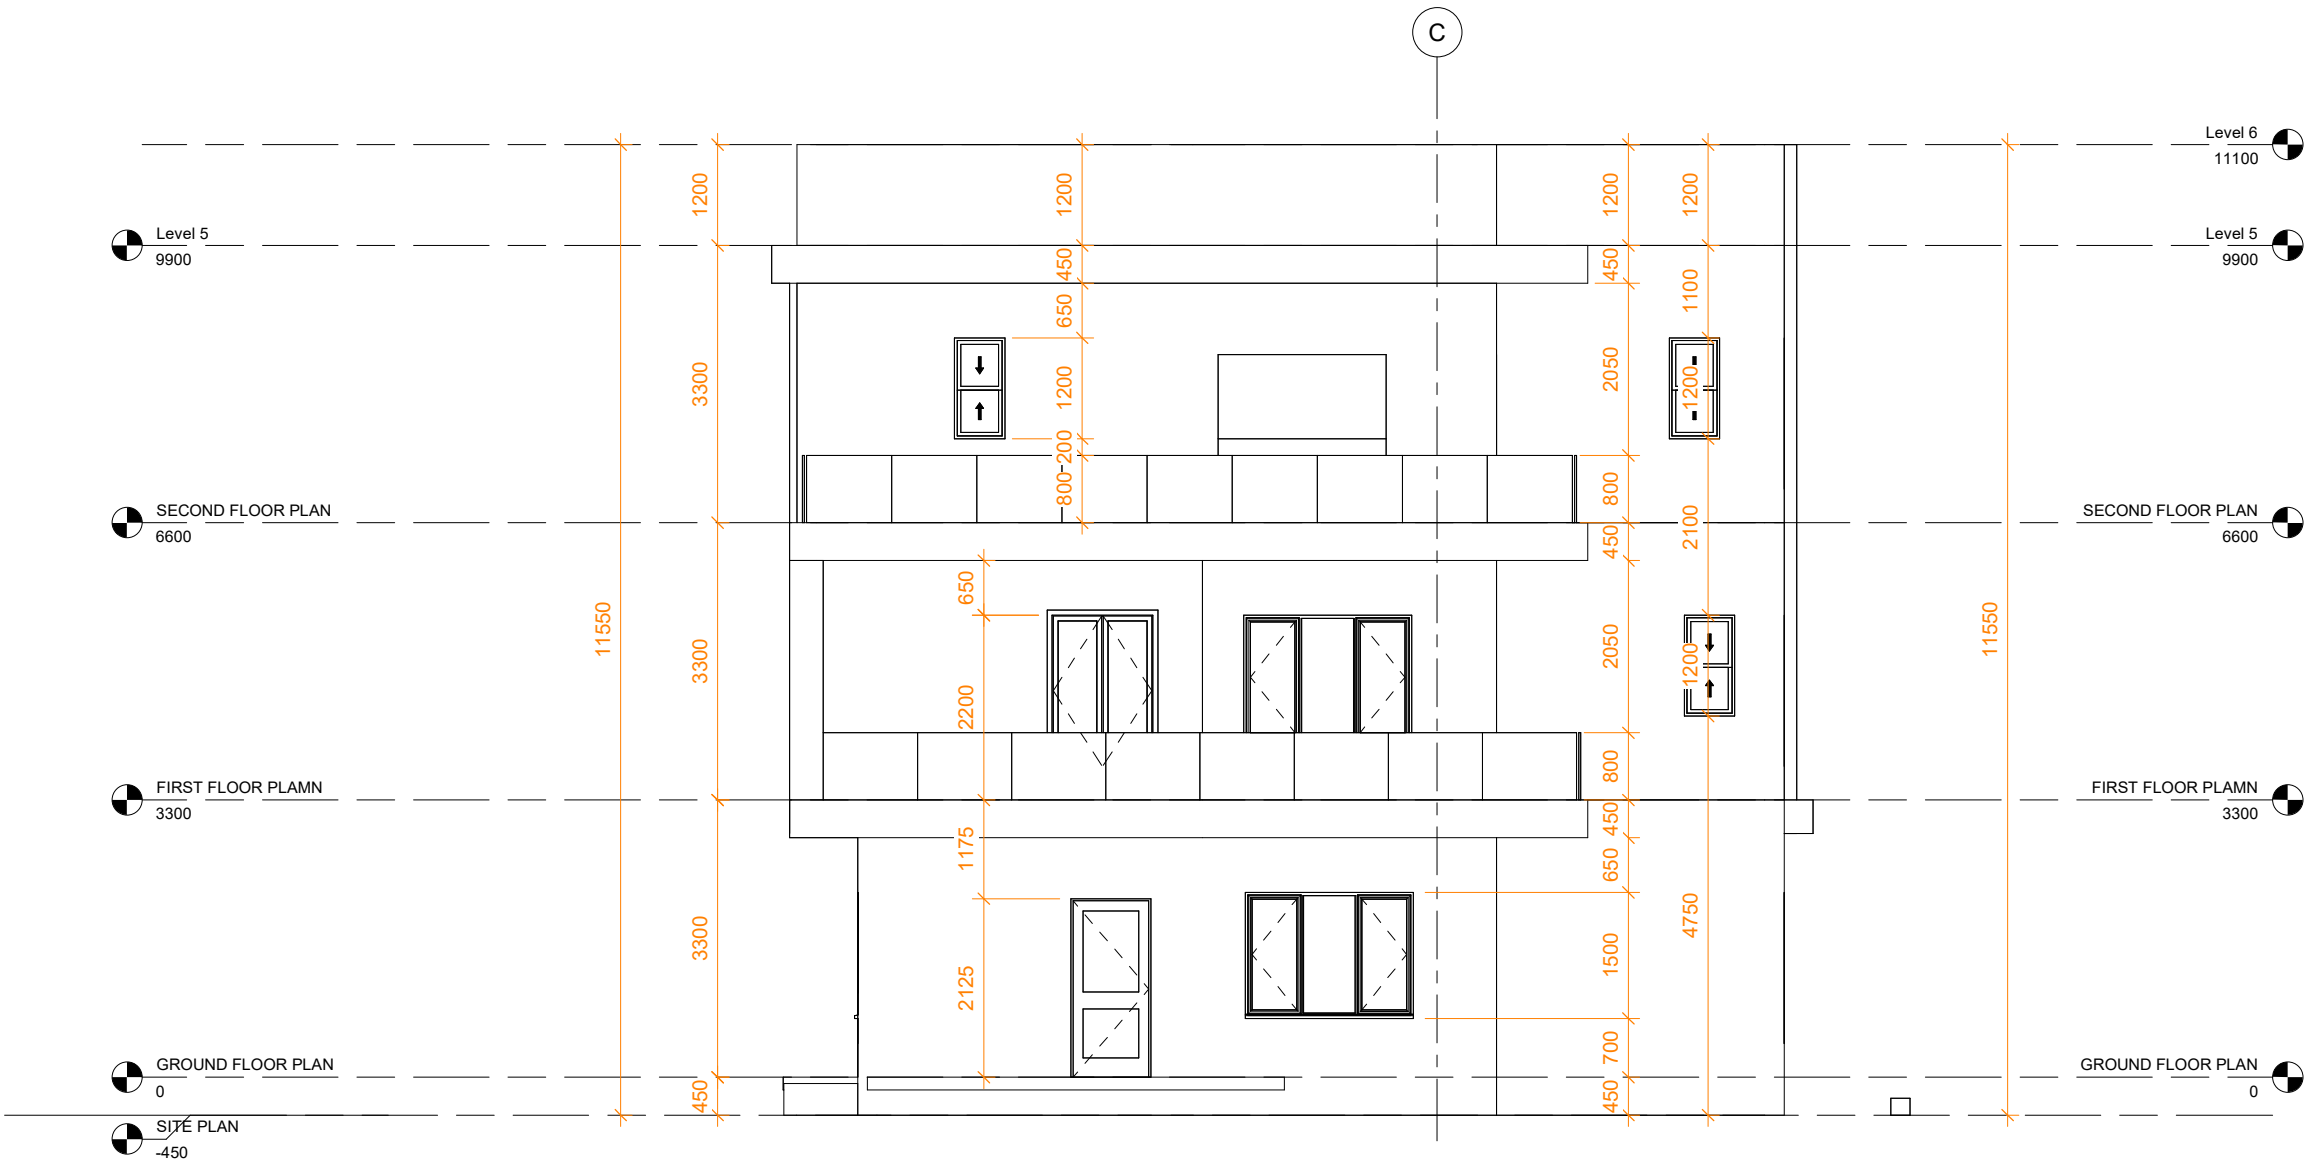

1 BACK ELEVATION
1 : 45

NOTES

SEAC
ARCHITECTS



No.	Description	Date

PROJECT NAME

PROPOSED RESIDENTIAL
DEVELOPMENT

PROJECT ADDRESS

LP. KN 51
NO. I-II, GIGINYU LG, KANO STATE.

CLIENT

ABDULMANAF YUNUSA

Designed By: ARC. Mustapha Shehu Usman

Checked by: Arc. Shehu Usman

Date: MARCH, 2024.

Contact: 08060092211

email: mskainuwa@gmail.com

Scale